电-19299/14

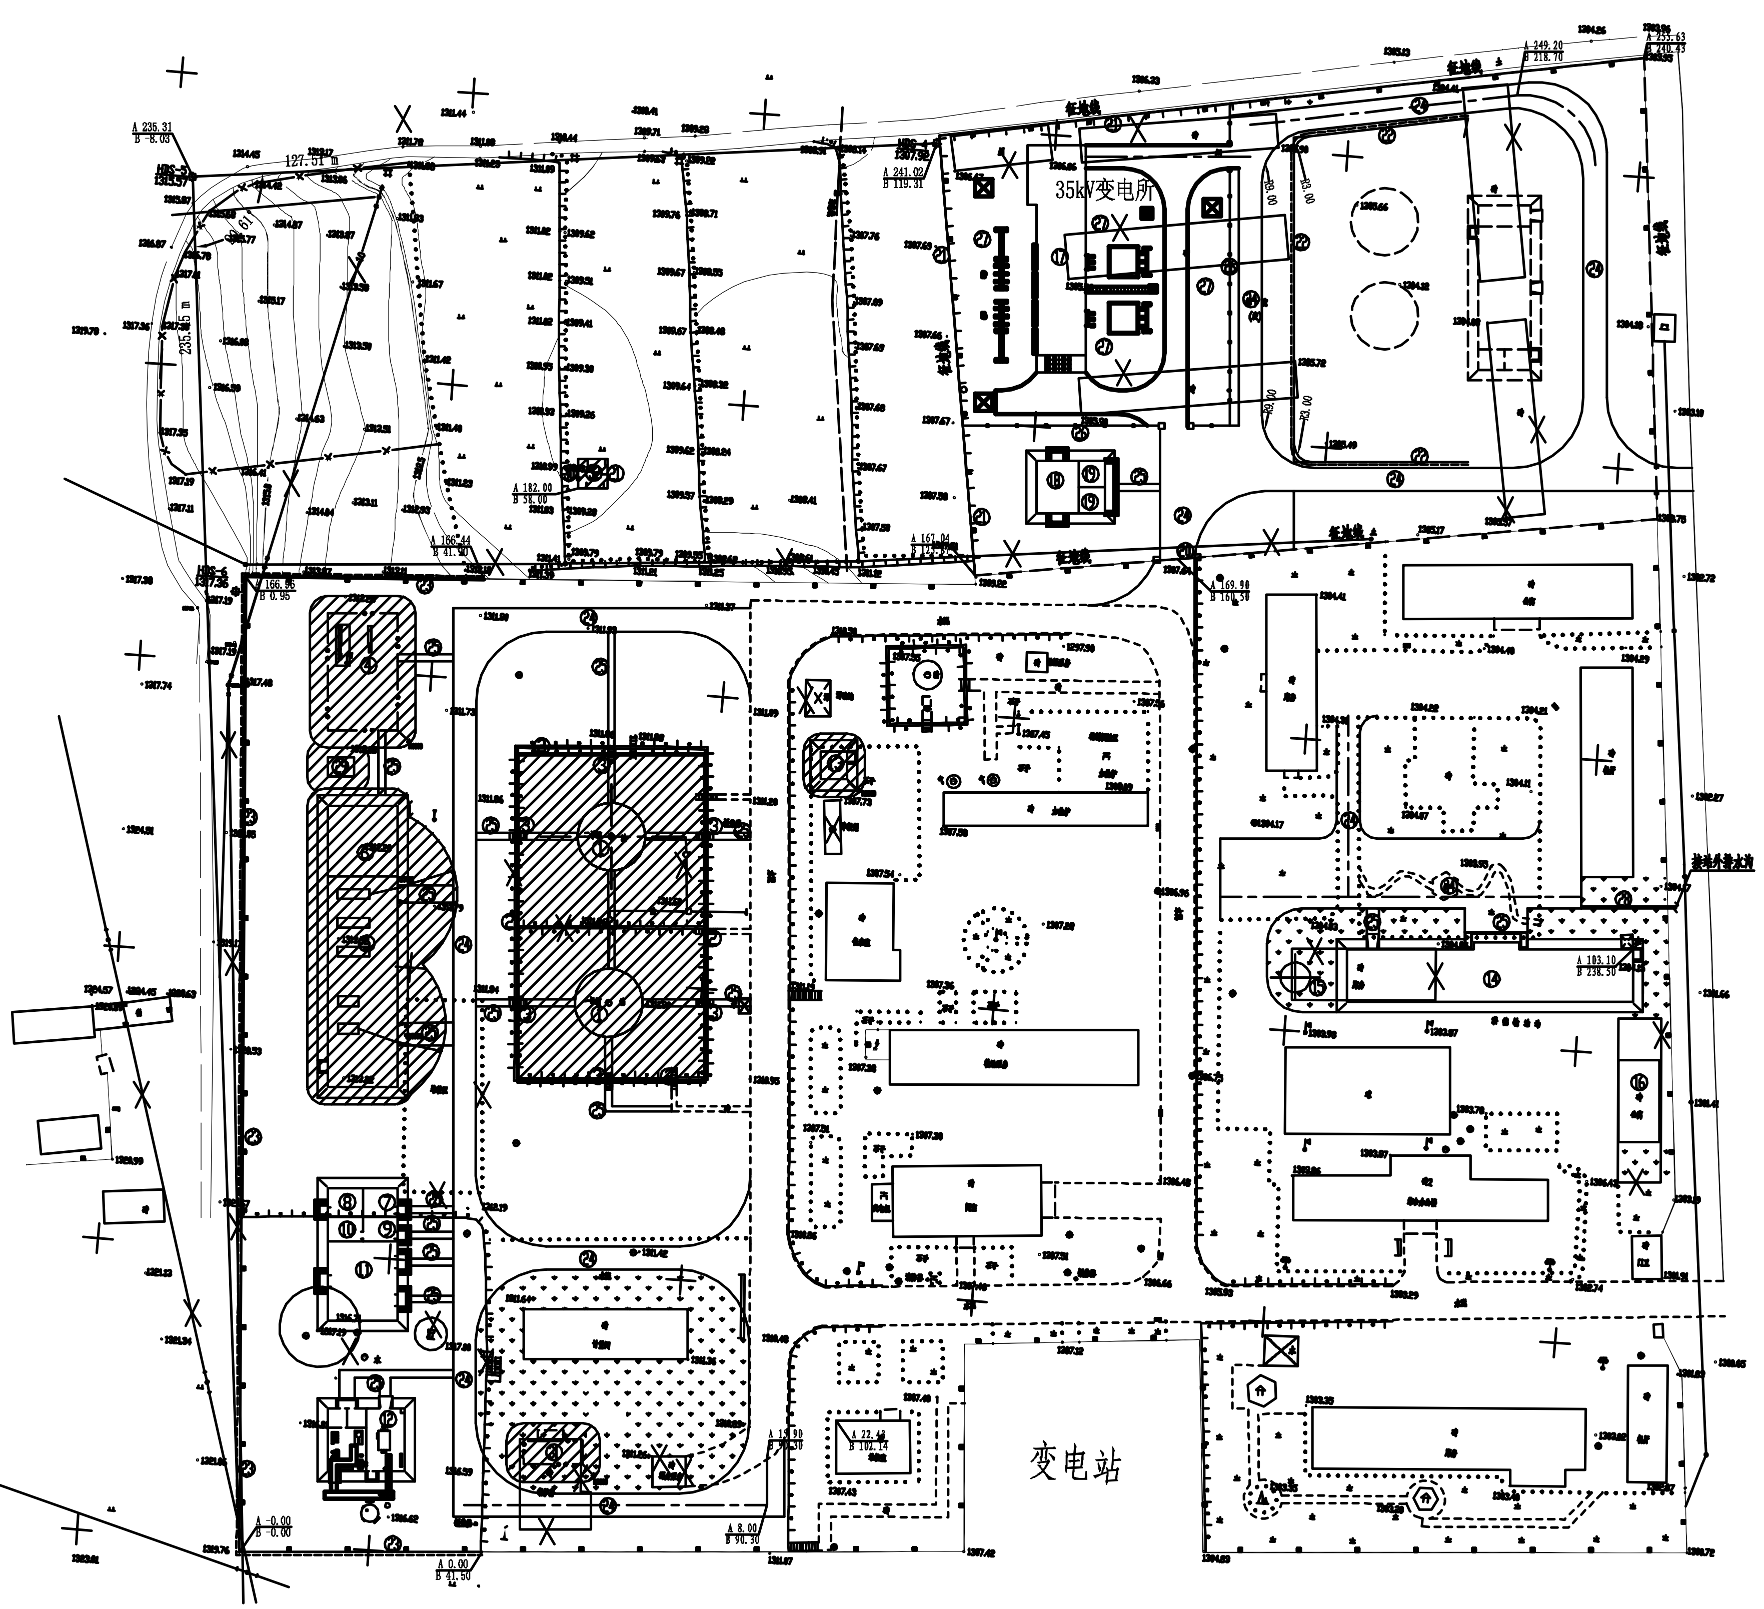

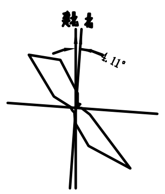

说明

1.《爆炸和火灾危险环境电力装置设计规范》(GB 50058-92)、《石油设施电气设备安装区域一级、0区、1区和2区区域划分推荐做法》(SY/T6671-2006)绘制。

2.图中释放源，通风条件见图例。

3.主要介质为石油 级别IIA级 组别T3

4.图例

▩ 1区　　▨ 2区

5.2区未标注范围半径均为3000mm。

6.爆炸危险区域内地坪下的坑、沟内顶部区域应为1区。

7.防爆区域内电缆敷设完毕后电缆沟应填沙，且进出建筑物房间处应进行密封封堵。

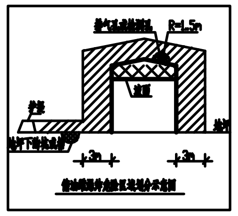

储油罐爆炸危险区域划分示意图

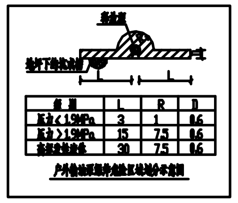

级别	L	R	D
压力＜1.9MPa	3	1	0.6
压力＞1.9MPa	15	7.5	0.6
高挥发性液体	30	7.5	0.6

户外输油泵爆炸危险区域划分示意图

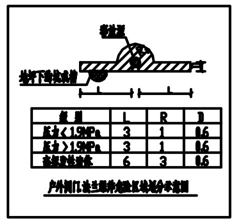

级别	L	R	D
压力＜1.9MPa	3	1	0.6
压力＞1.9MPa	3	1	0.6
高挥发性液体	6	3	0.6

户外阀门、法兰爆炸危险区域划分示意图

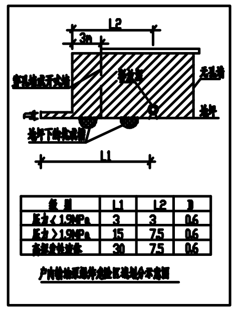

级别	L1	L2	D
压力＜1.9MPa	3	3	0.6
压力＞1.9MPa	15	7.5	0.6
高挥发性液体	30	7.5	0.6

户内输油泵爆炸危险区域划分示意图

编号	名称及规格	单位	数量	文件号	备注
㉜	放空区　5m×5m	m²	25	建-29421/II	水泥方砖铺砌
㉛	配气区　4m×10m	m²	40	建-29421/II	水泥方砖铺砌
㉚	钢大门　宽1.2m	樘	1	建-29421/II	
㉙	污油池　4.5m×3.3m	m²	14.85	建-29421/II	水泥方砖铺砌
㉘	砖砌排水明沟　宽0.4m，起点深0.2m	m	106	建-29421/II	
㉗	变电所铺砌场地	m²	1660	建-29421/II	渗水砖铺砌
㉖	铁艺围栏　高1.5m	m	110	建-29421/II	
㉕	人行道及操作通道　宽1.2m	m²	789.6	建-29421/II	水泥方砖铺砌
㉔	站内道路　宽4m	m²	3847.6	建-29421/II	城市型混凝土道路
㉓	挡土墙II　地面部分高0.5m~10.3m	m	274.2	建-29421/II	
㉒	挡土墙I　地面部分高0.5m~3m	m	125.8	建-29421/II	
㉑	新建砖砌围墙　高2.5m	m	187	建-29421/II	
⑳	钢大门　宽6m	樘	1	建-29421/II	
⑲	变压器室　4.5m×4.5m	m²	20.25	建-29421/II	框架结构
⑱	低压配电室　4.5m×9m	m²	40.5	建-29421/II	框架结构
⑰	35kV变电所综合楼　39m×9.9m	m²	386.1	建-29421/II	框架结构
⑯	埋地污水处理装置	套	1		
⑮	100m³ 生活水罐	具	1		
⑭	新建宿舍　48.9m×9m	m²	440.1	建-29265/II	砖混结构
⑬	燃料油泵房　4.5m×4.8m	m²	21.6	建-29421/II	钢架结构
⑫	锅炉房　13.2m×10.8m	m²	142.56	建-29421/II	框架结构
⑪	变频器室　13.5m×12m	m²	162	建-29421/II	框架结构
⑩	阴保间　6m×4.2m	m²	25.2	建-29421/II	框架结构
⑨	工具间　6m×4.2m	m²	25.2	建-29421/II	框架结构
⑧	仪表机柜间　6m×5m	m²	30	建-29421/II	框架结构
⑦	值班室　6m×5m	m²	30	建-29421/II	框架结构
⑥	阀组间　12m×12m	m²	144	建-29421/II	钢架结构
⑤	外输泵房　36m×12m	m²	432	建-29421/II	钢架结构
④	收发球区　12m×20m	m²	240	建-29421/II	水泥方砖铺砌
③	防火堤踏步　高1.9m，宽1m	处	6	建-29421/II	砖砌结构
②	防火堤　高1.9m	m	186	建-29421/II	钢筋混凝土
①	1000m³ 储油罐	具	2		已建

建(构)筑物一览表

西安长庆科技工程有限责任公司
(长庆勘察设计研究院)
设计证书号 A161000224　　勘察证书号 260602-kj

制图	
设计	
校对	
审核	

马惠原油管道安全升级改造工程

洪德热泵站
爆炸危险区域划分图

阶段	施工图	项目号	CTBC188S-2013		
比例	1:500	文件号	电-19299/14		
日期	2014.08.04	专业	电气	版次	1 版

PDF 文件使用 "pdfFactory Pro" 试用版本创建 www.fineprint.cn