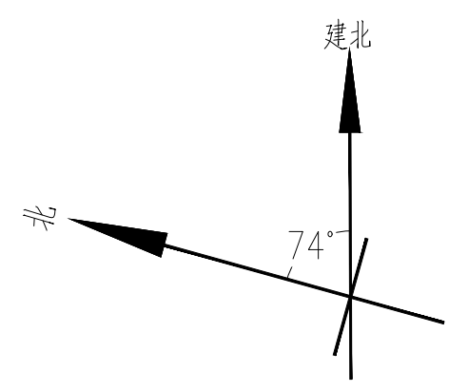

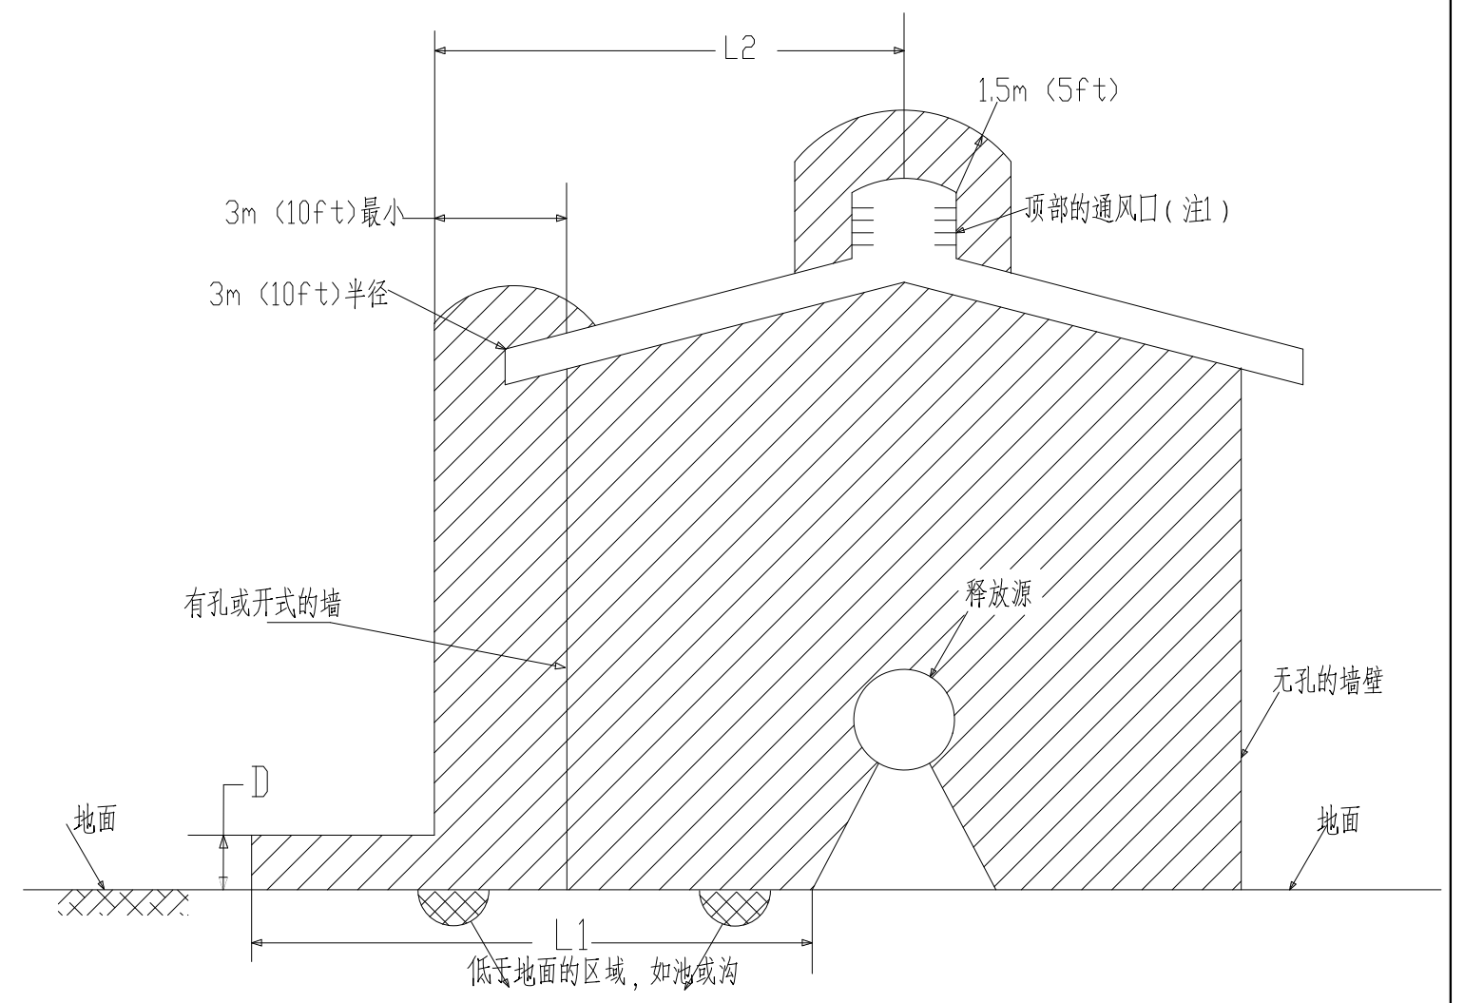

等级	距离，m(ft)		
	L1	L2	D
1.液体表压为1900KPa(275psig)或更低	3(10)	3(10)	0.6(2)
2.液体表压高于1900KPa(275psig) (注2)	15(50)	7.5(25)	0.6(2)
3.HVL(注3)	30(100)	7.5(25)	0.6(2)

说明：

1. 由于释放源位置无法确定，爆炸危险区域以工艺装置区边界进行划分。
2. 依据图根据《石油设施电气设备场所I级0区、1区和2区的分类推荐作法》(SYT 6671-2017)及《爆炸危险环境电力装置设计规范》(GB50058-2014)绘制。
3. 爆炸危险区域内地坪下的坑内应为1区，其余为2区。
4. 图例:

0区	1区	2区
⬡	☒	▨

5. 释放源主要为石油，所属组别为IIA，温度组别为T3。
6. 图中半径标注以米为计。

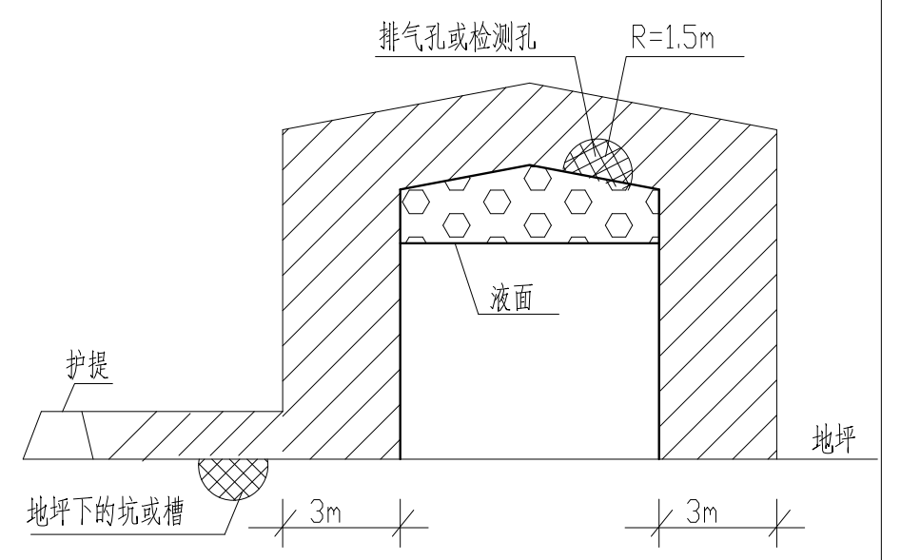

储油罐爆炸危险区域划分示意图

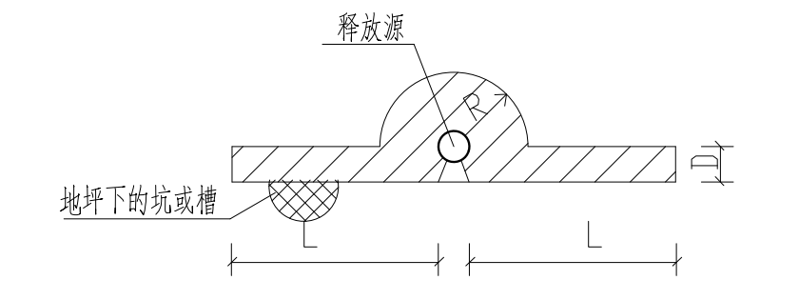

级 别	L	R	D
压力≤1.9MPa	3	1	0.6
压力>1.9MPa	3	1	0.6
高挥发性液体	6	3	0.6

户外阀门.法兰爆炸危险区域划分示意图

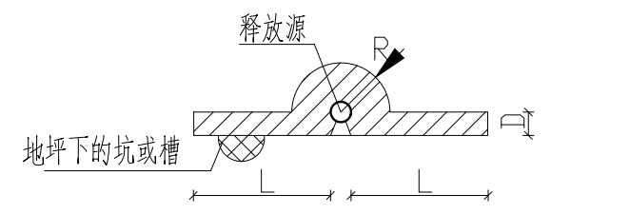

级 别	L	R	D
压力≤1.9MPa	3	1	0.6
压力>1.9MPa	15	7.5	0.6
高挥发性液体	30	7.5	0.6

室外—输送易燃液体或高挥发性液体的
压缩机或泵爆炸危险区域划分示意图

中国石油天然气管道工程有限公司
CHINA PETROLEUM PIPELINE ENGINEERING CORPORATION
工程设计综合甲级证书编号A113A00237　工程勘察综合甲级证书编号B113A00237

制 图	刘金凤	长庆油田分公司第二输油处2026年维修工程
设 计	刘金凤	
校 对	葛露萍	场站爆炸危险区域划分 电气部分 白豹输油站爆炸危险区域划分图
审 核		

阶 段	施工图	文件号	DWG-0201EL01-001
比 例	1:250	项目号	DD26174
日 期	2026.4.16	版 次	0

DWG-0201EL01-002

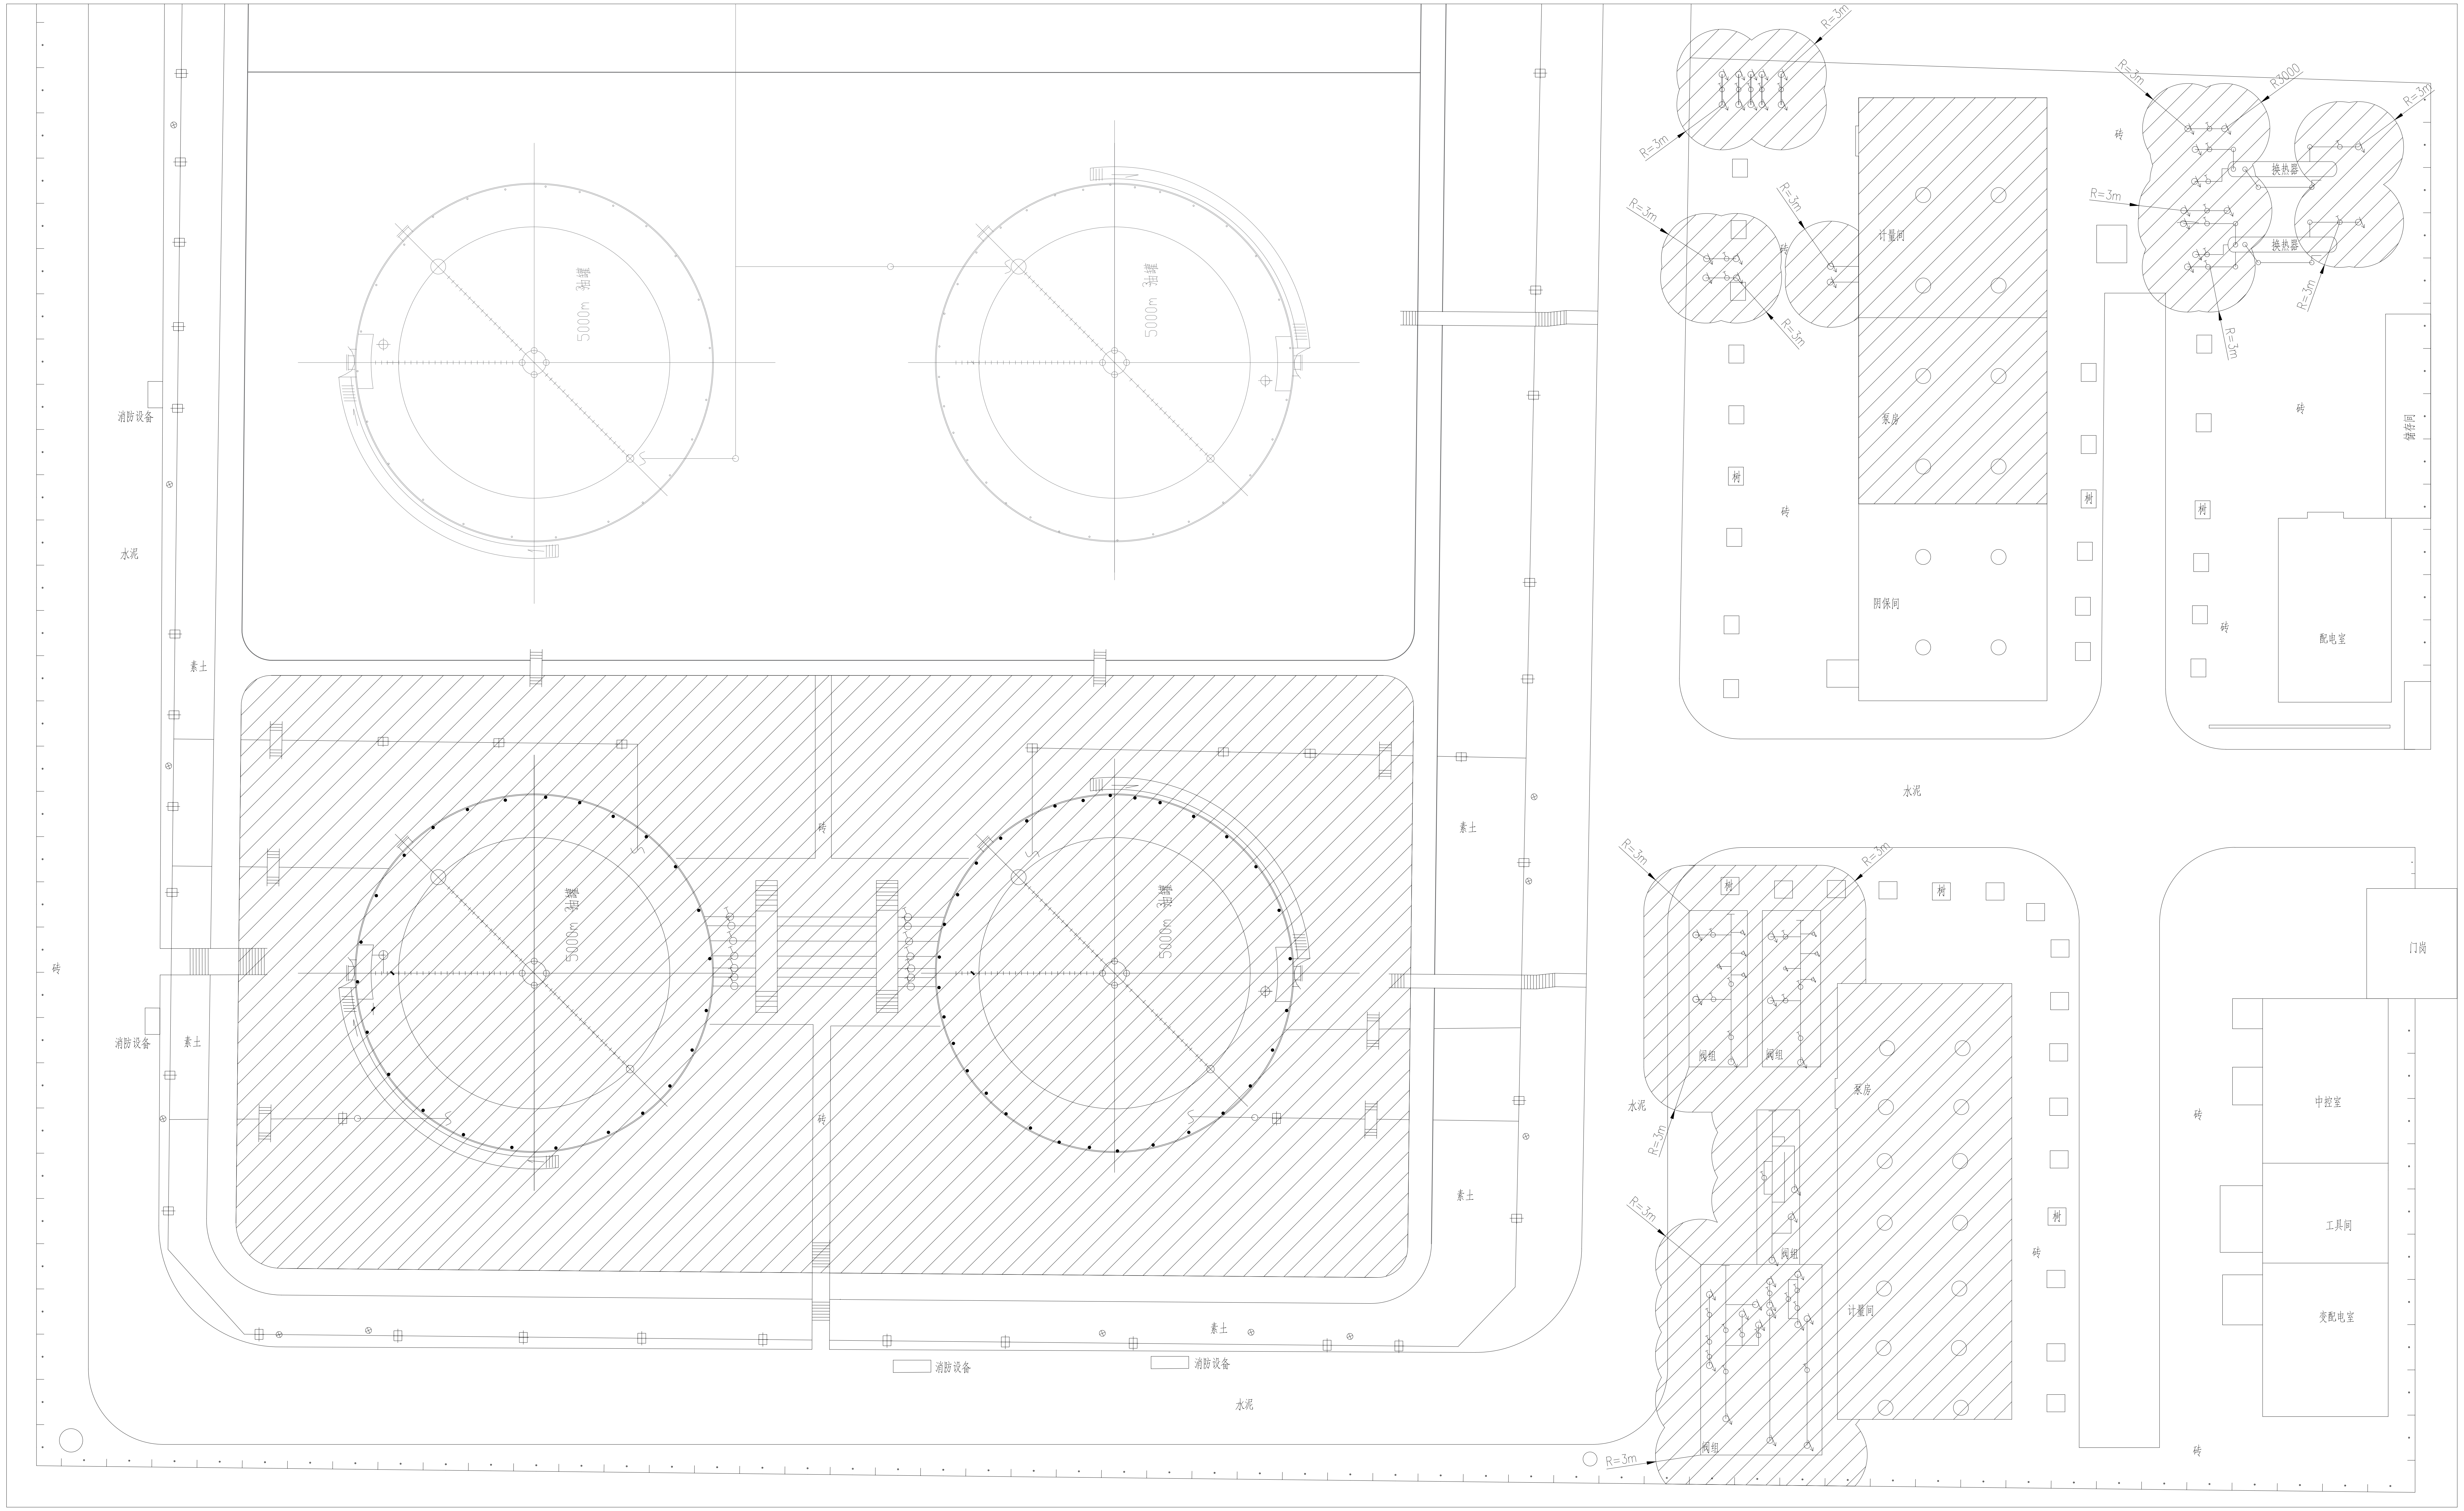

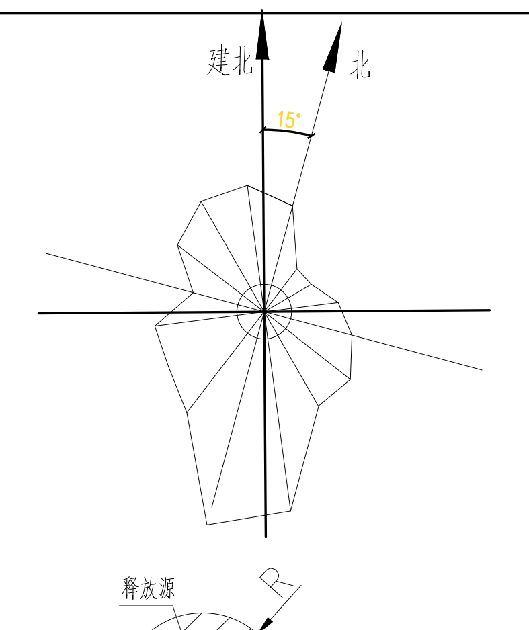

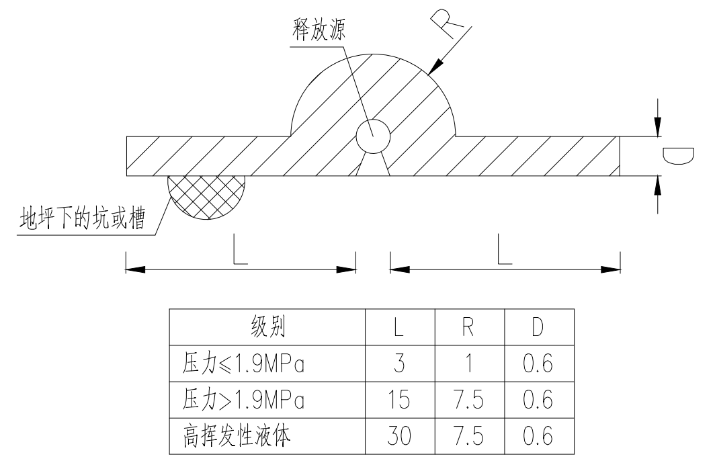

级别	L	R	D
压力≤1.9MPa	3	1	0.6
压力>1.9MPa	15	7.5	0.6
高挥发性液体	30	7.5	0.6

室外－输送易燃液体或高挥发性液体的泵或压缩机爆炸危险区域划分示意图

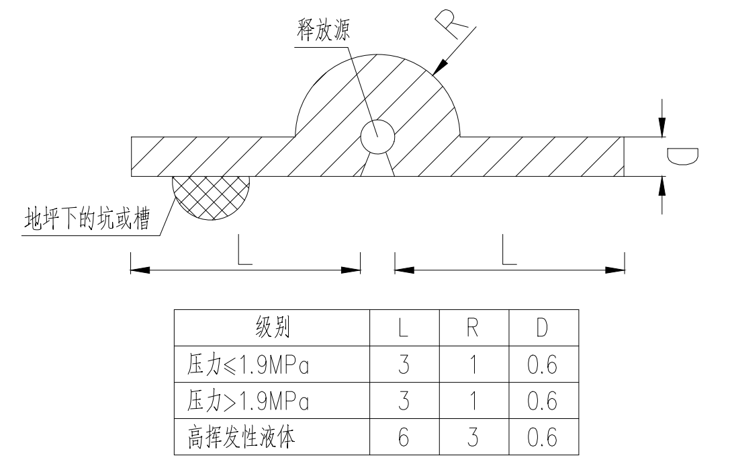

级别	L	R	D
压力≤1.9MPa	3	1	0.6
压力>1.9MPa	3	1	0.6
高挥发性液体	6	3	0.6

户外阀门、法兰爆炸危险区域划分示意图

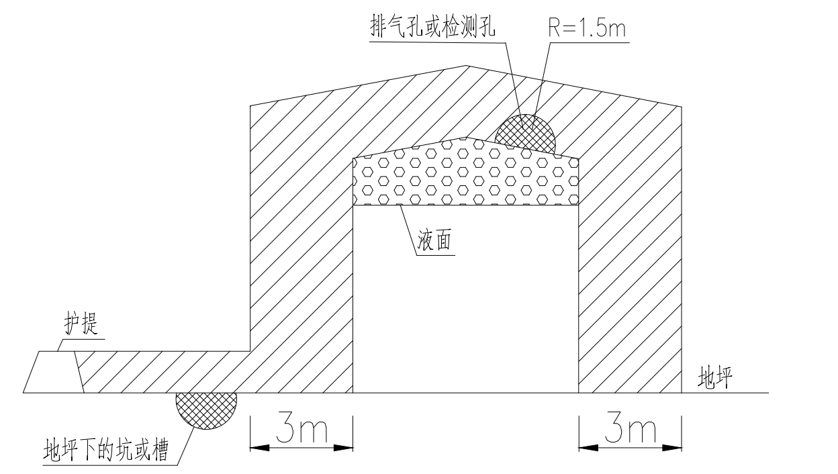

储油罐爆炸危险区域划分示意图

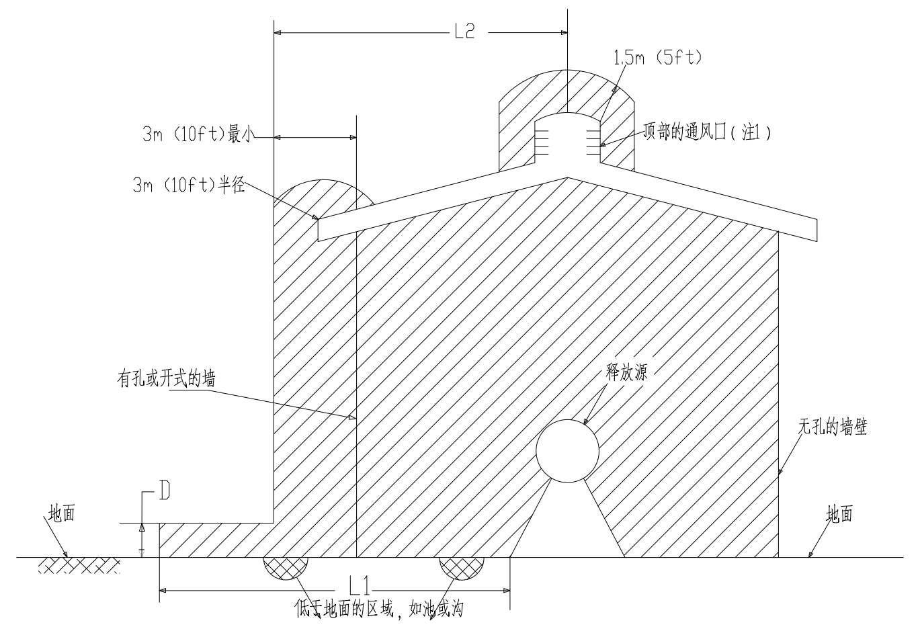

等级	距离，m(ft)		
	L1	L2	D
1.液体表压为1900KPa(275psig)或更低	3(10)	3(10)	0.6(2)
2.液体表压高于1900KPa(275psig) (注2)	15(50)	7.5(25)	0.6(2)
3.HVL(注3)	30(100)	7.5(25)	0.6(2)

说明：

1）本图根据《爆炸危险环境电力装置设计规范》(GB50058-2014)、《石油设施电气设备场所Ⅰ级0区、1区和2区的分类推荐作法》(SYT6671-2017)中有关规定进行绘制。

2）本次改造爆炸危险区域内地坪下的坑内应为1区，其余为2区，2区未标注范围半径均为3m。

3）释放源主要为石油，所属组别为IIA，温度组别为T3。

4）图例

▦0区 ▩1区 ▨2区

中国石油天然气管道工程有限公司
CHINA PETROLEUM PIPELINE ENGINEERING CORPORATION
工程设计综合甲级证书编号A113A00237 工程勘察综合甲级证书编号B113A00237

制　图	葛露萍	长庆油田分公司第二输油处2026年维修工程
设　计	葛露萍	场站爆炸危险区域划分 电气部分 铁西末站爆炸危险区域划分图
校　对	刘金凤	
审　核		

阶　段	施工图	文件号	DWG-0201EL01-002
比　例	1:200	项目号	DD26174
日　期	2026.04.16	版　次	0

DWG-0201EL01-003

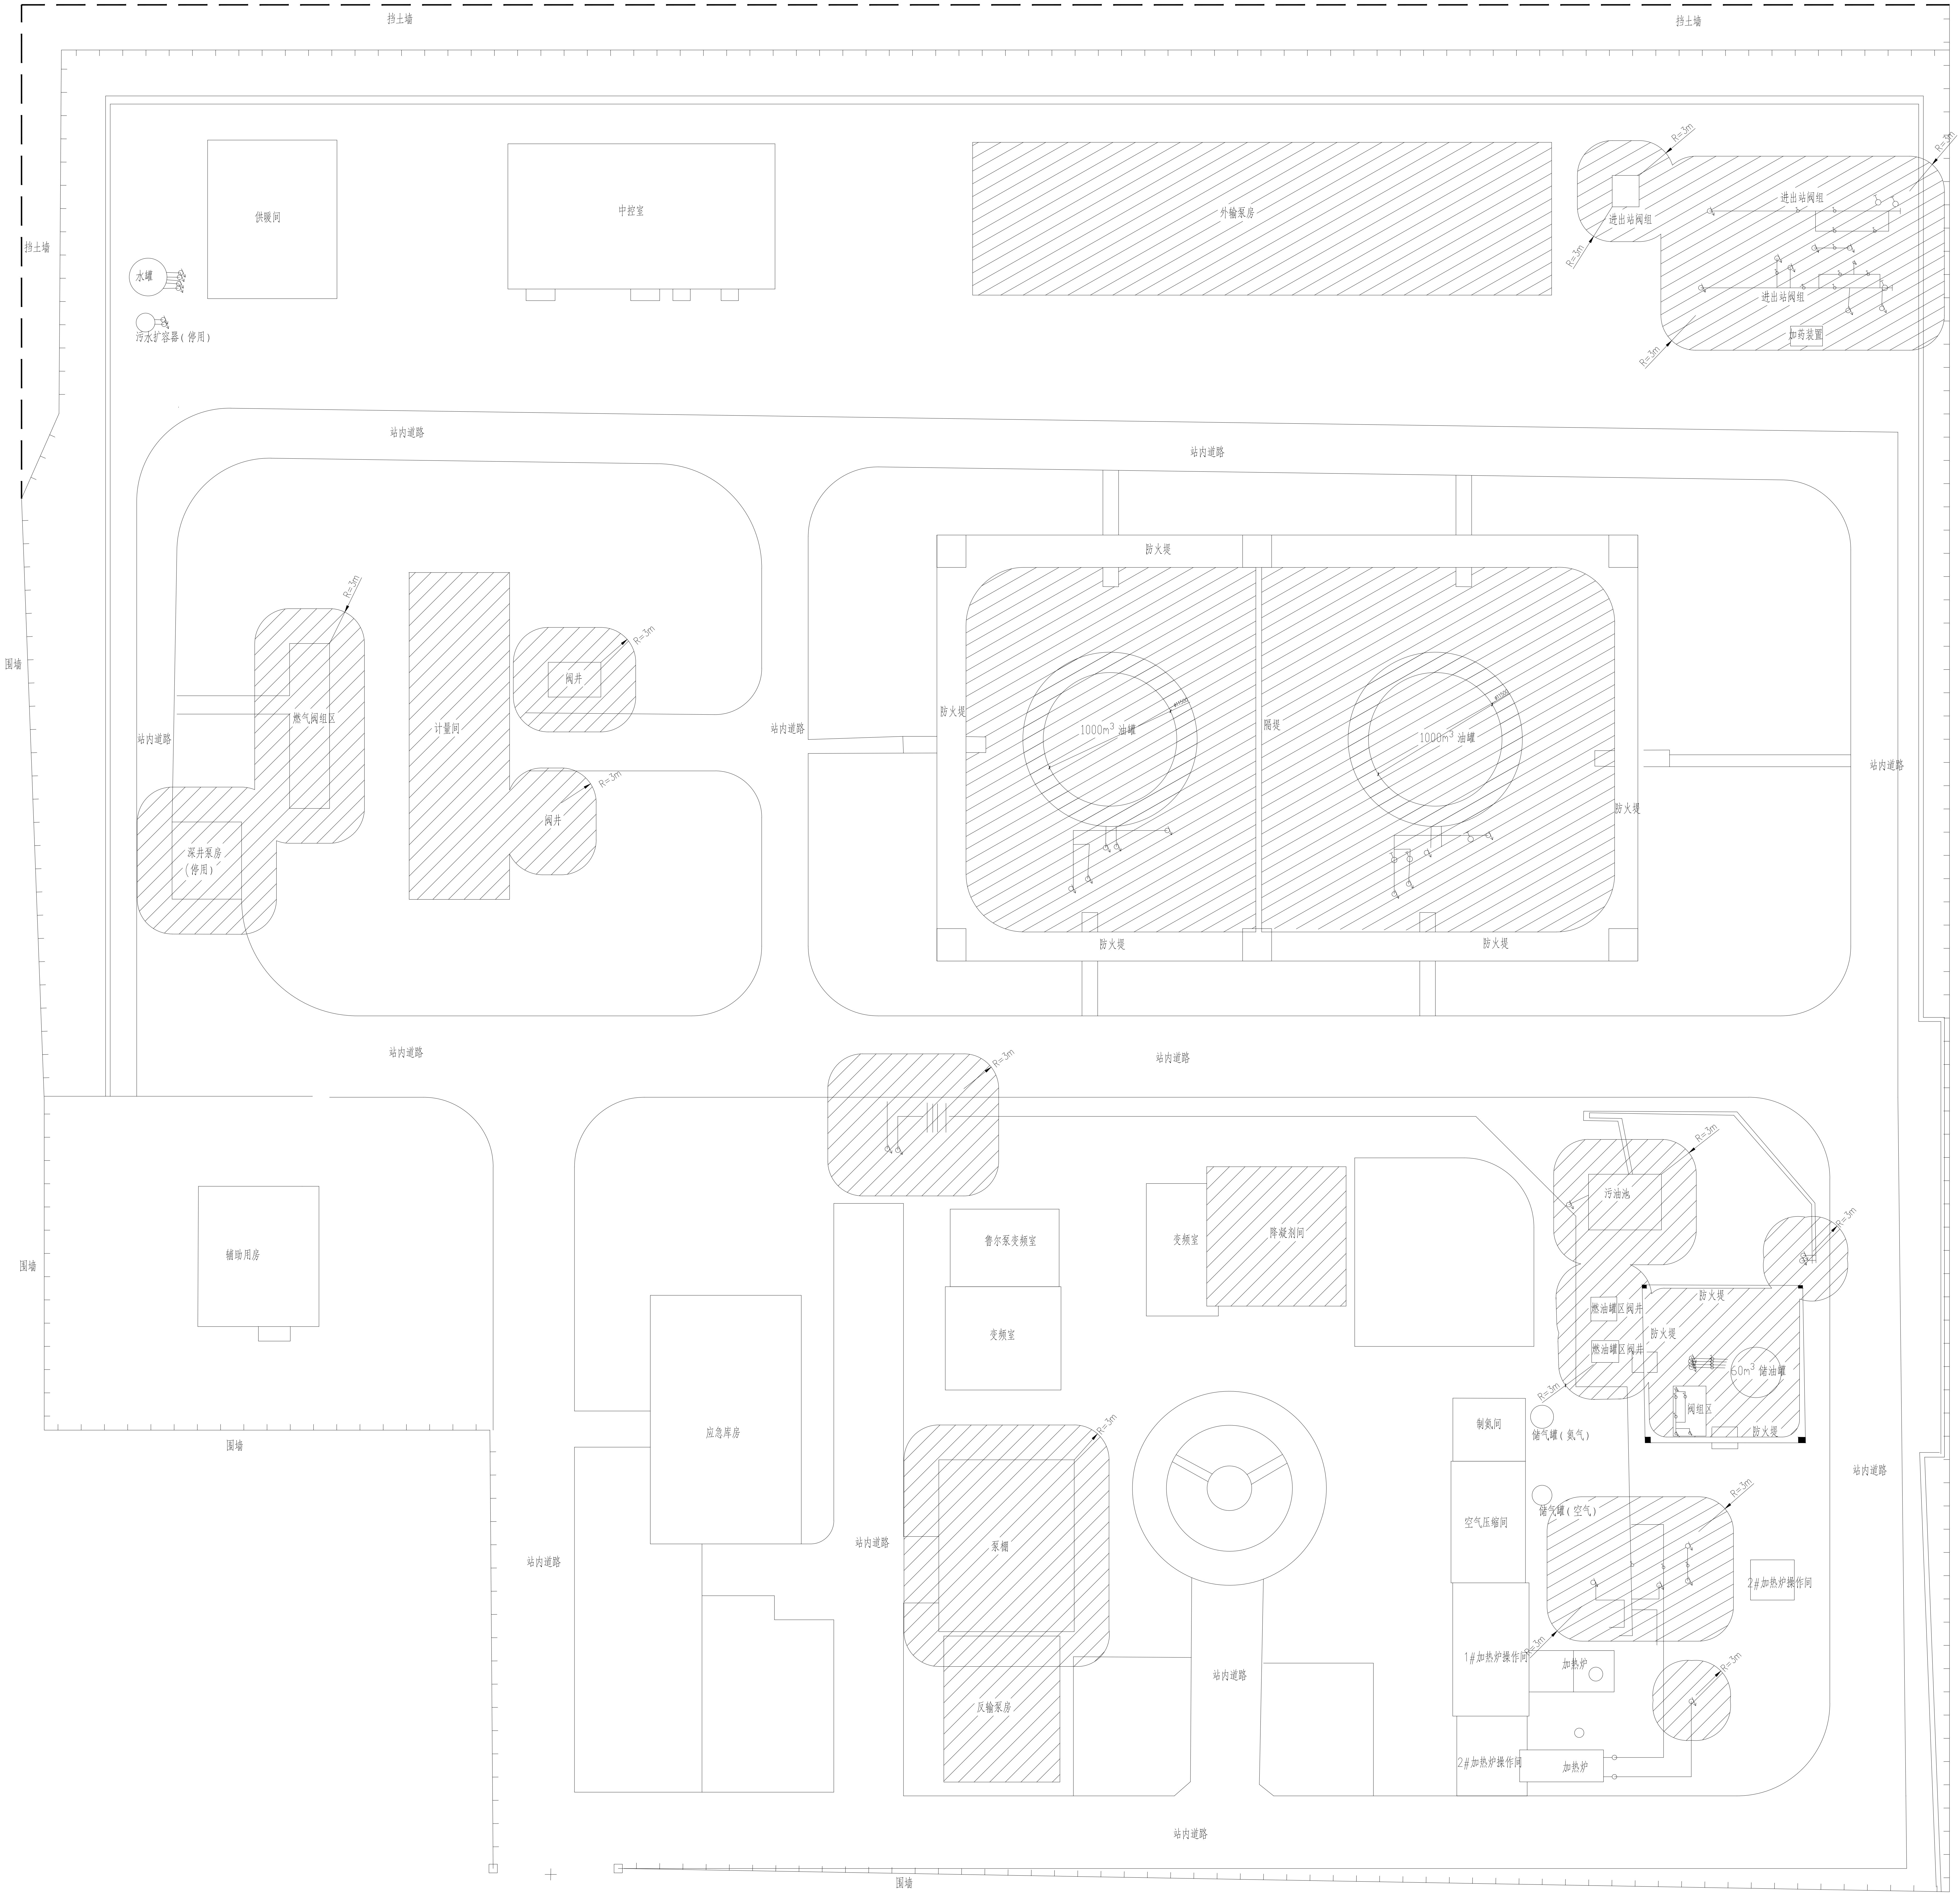

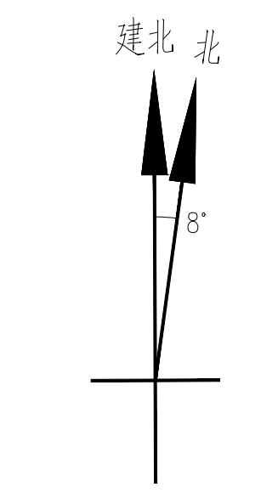

说明：

1. 由于释放源位置无法确定，爆炸危险区域以工艺装置区边界进行划分。
2. 依据图根据《石油设施电气设备场所Ⅰ级0区、1区和2区的分类推荐作法》(SYT 6671-2017)及《爆炸危险环境电力装置设计规范》（GB50058-2014）绘制。
3. 爆炸危险区域内地坪下的坑内应为1区，其余为2区。
4. 图例:

▨ 0区　▨ 1区　▨ 2区

5. 释放源主要为石油，所属组别为IIA，温度组别为T3。
6. 图中半径标注以米为计。

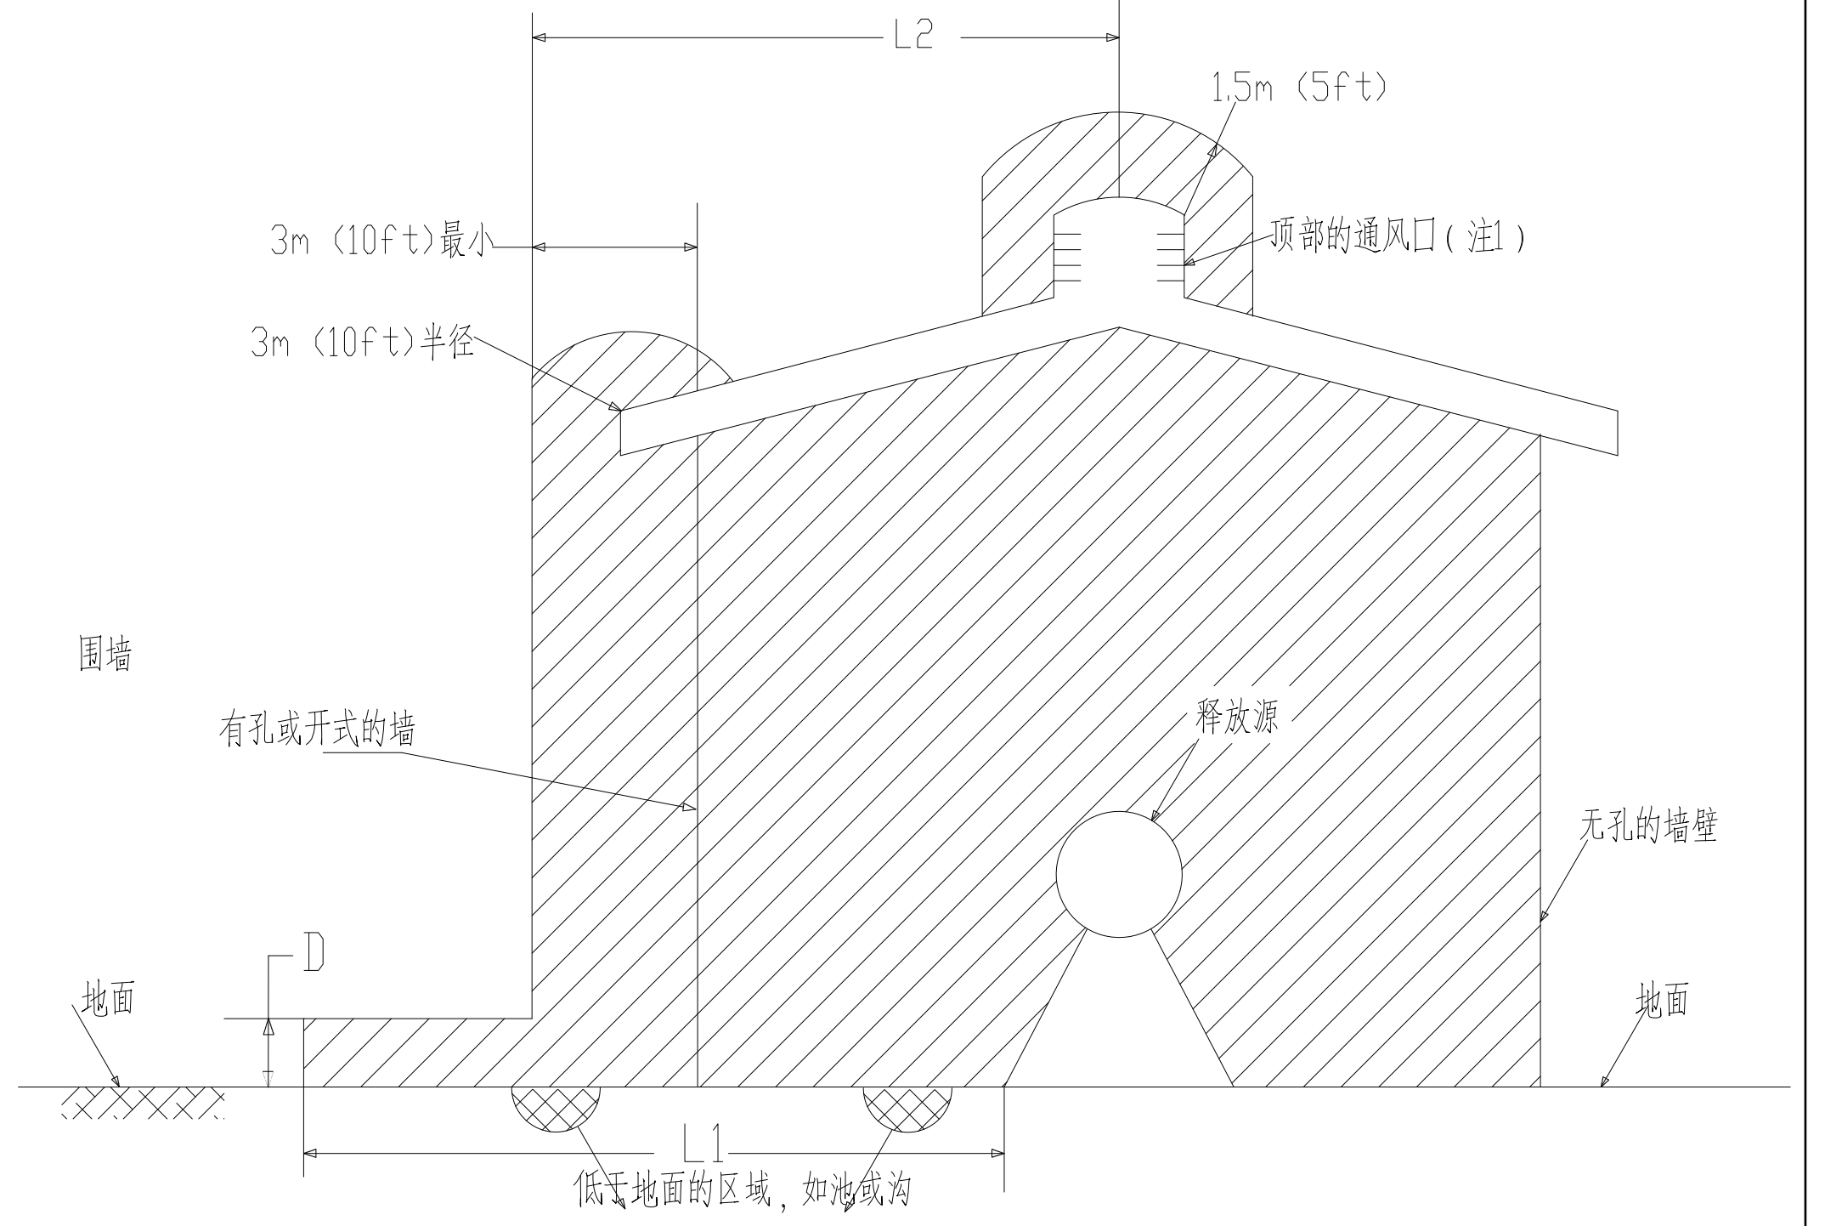

等级	距离，m（ft）		
	L1	L2	D
1.液体表压为1900KPa（275psig）或更低	3（10）	3（10）	0.6（2）
2.液体表压高于1900KPa（275psig）（注2）	15（50）	7.5（25）	0.6（2）
3.HVL（注3）	30（100）	7.5（25）	0.6（2）

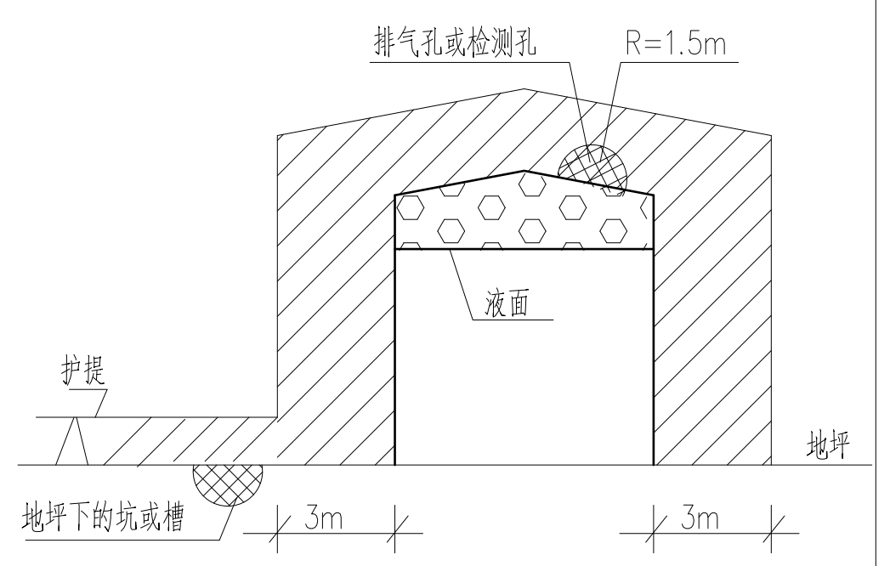

储油罐爆炸危险区域划分示意图

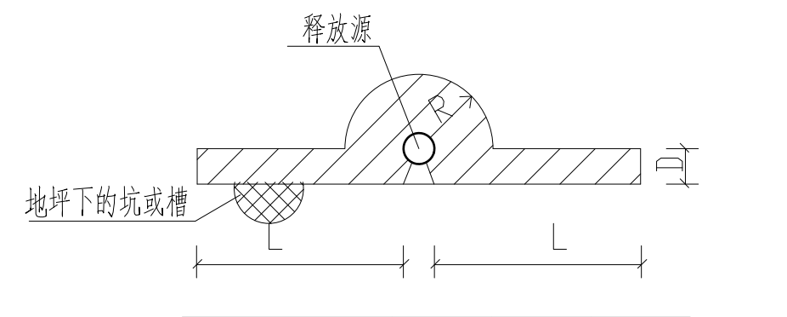

级 别	L	R	D
压力≤1.9MPa	3	1	0.6
压力>1.9MPa	3	1	0.6
高挥发性液体	6	3	0.6

户外阀门.法兰爆炸危险区域划分示意图

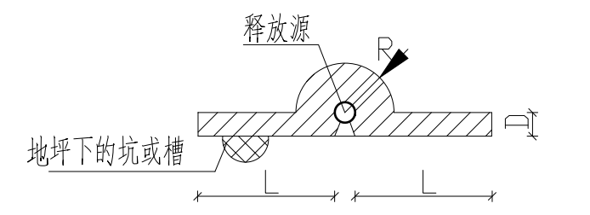

级 别	L	R	D
压力<1.9MPa	3	1	0.6
压力>1.9MPa	15	7.5	0.6
高挥发性液体	30	7.5	0.6

室外—输送易燃液体或高挥发性液体的
压缩机或泵爆炸危险区域划分示意图

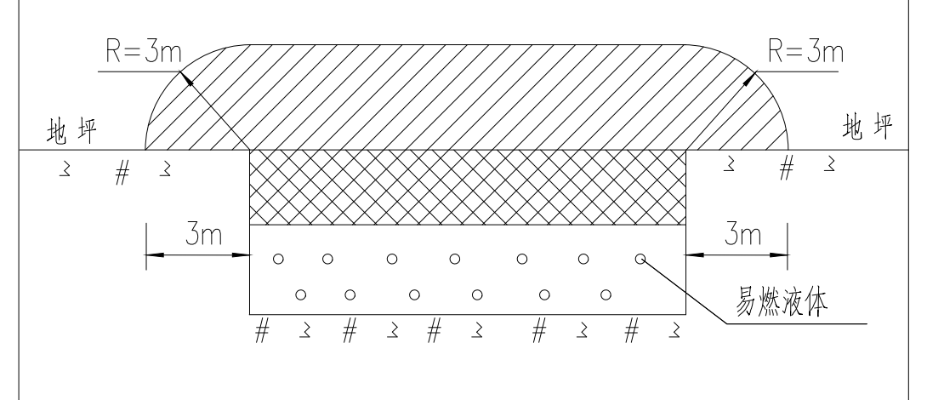

污油池爆炸危险区域划分示意图

中国石油天然气管道工程有限公司
CHINA PETROLEUM PIPELINE ENGINEERING CORPORATION
工程设计综合甲级证书编号A113A00237　工程勘察综合甲级证书编号B113A00237

制 图	杨麟淇	长庆油田分公司第二输油处2026年维修工程			
设 计	杨麟淇	场站爆炸危险区域划分 电气部分 洪德输油站爆炸危险区域划分图			
校 对	刘金凤				
审 核					
		阶 段	施工图	文件号	DWG-0201EL01-003
		比 例	1:200	项目号	DD26174
		日 期	2026.4.16	版 次	0

DWG-0201EL01-004

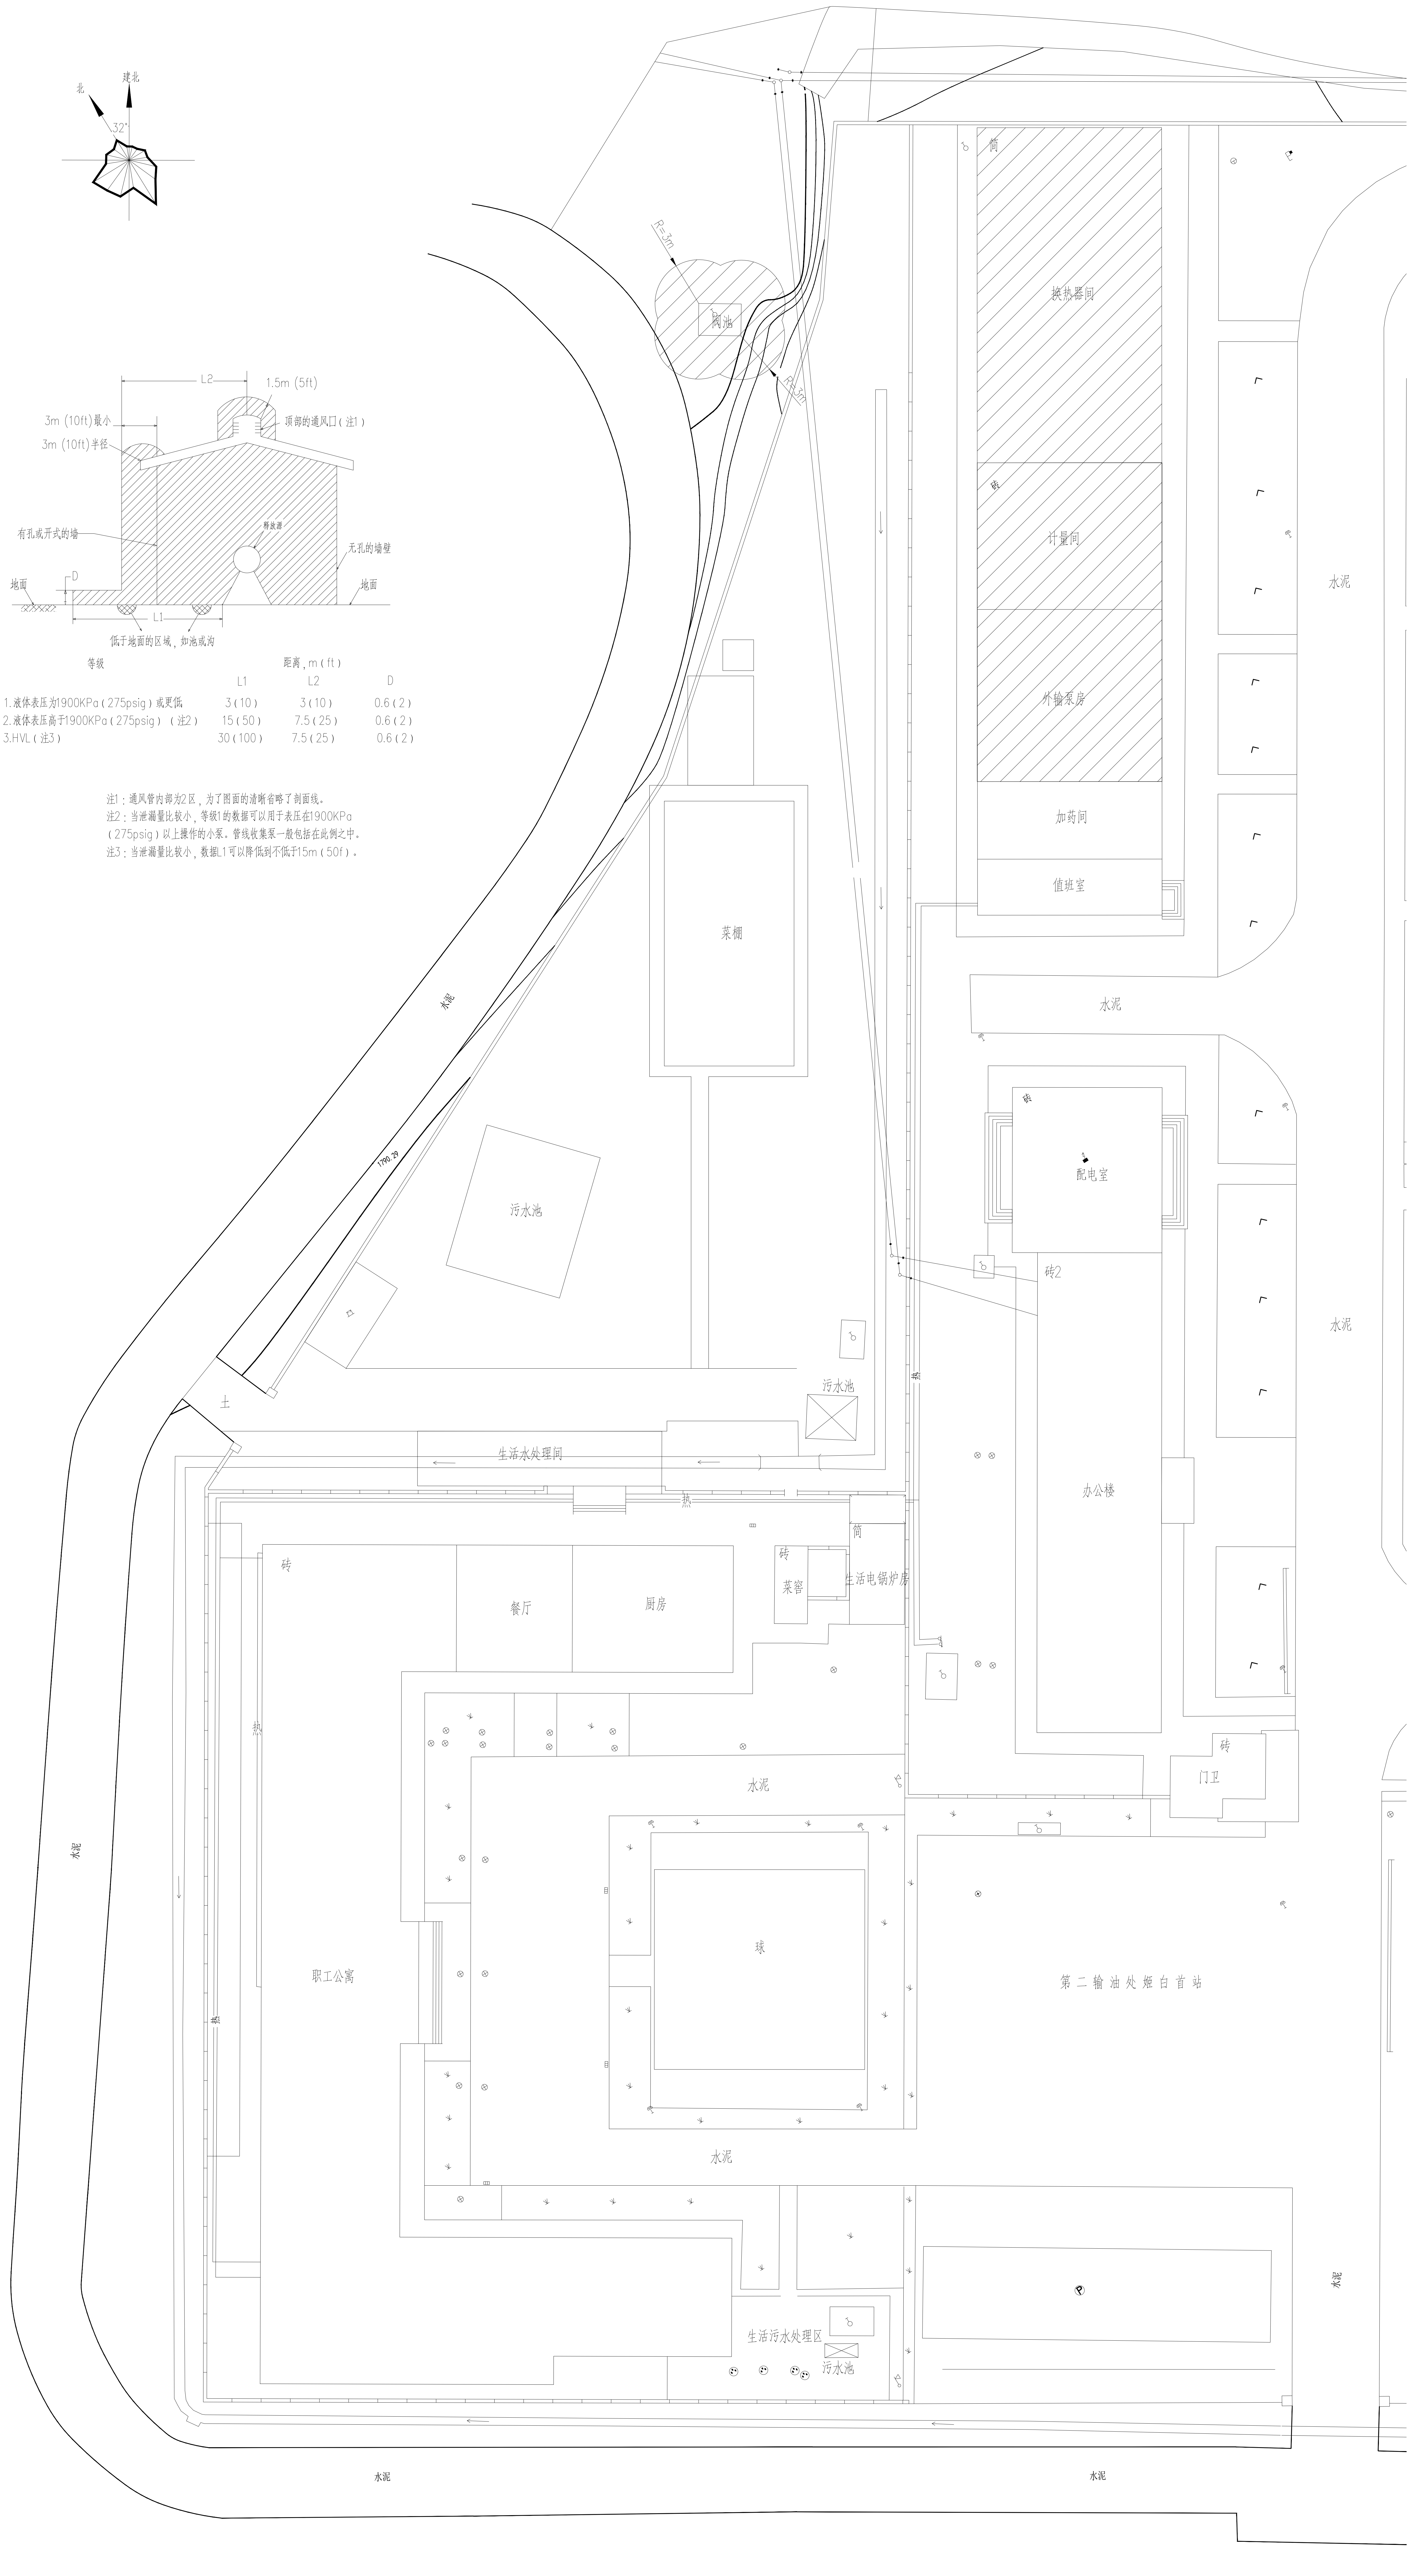

等级	距离，m（ft） L1	L2	D
1.液体表压为1900KPa（275psig）或更低	3（10）	3（10）	0.6（2）
2.液体表压高于1900KPa（275psig）（注2）	15（50）	7.5（25）	0.6（2）
3.HVL（注3）	30（100）	7.5（25）	0.6（2）

注1：通风管内部为2区，为了图面的清晰省略了剖面线。
注2：当泄漏量比较小，等级1的数据可以用于表压在1900KPa（275psig）以上操作的小泵。管线收集泵一般包括在此例之中。
注3：当泄漏量比较小，数据L1可以降低到不低于15m（50f）。

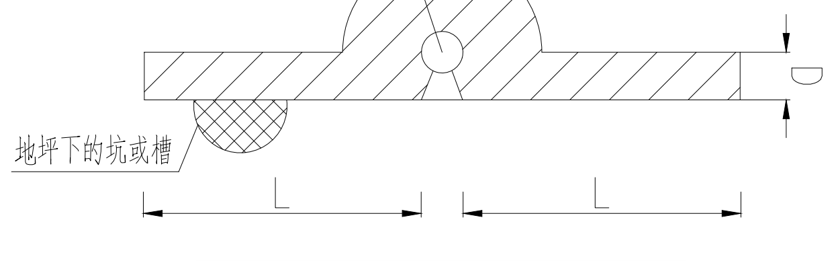

级别	L	R	D
压力≤1.9MPa	3	1	0.6
压力>1.9MPa	3	1	0.6
高挥发性液体	6	3	0.6

户外阀门、法兰爆炸危险区域划分示意图

说明：

1）本图根据《爆炸危险环境电力装置设计规范》（GB50058-2014）、《石油设施电气设备场所I级0区、1区和2区的分类推荐作法》（SYT6671-2017）中有关规定进行绘制。

2）本次改造爆炸危险区域内地坪下的坑内应为1区，其余为2区，2区未标注范围半径均为3m。

3）释放源主要为石油，所属组别为IIA，温度组别为T3。

4）图例

- ⁘ 0区
- ▩ 1区
- ▨ 2区

中国石油天然气管道工程有限公司
CHINA PETROLEUM PIPELINE ENGINEERING CORPORATION
工程设计综合甲级证书编号A113A00237 工程勘察综合甲级证书编号B113A00237

制图	葛露萍	长庆油田分公司第二输油处2026年维修工程	
设计	葛露萍		
校对	刘金凤	场站爆炸危险区域划分 电气部分 姬白首站爆炸危险区域划分图	
审核			
阶段	施工图	文件号	DWG-0201EL01-004
比例	1:200	项目号	DD26174
日期	2026.04.16	版次	0

DWG-0201EL01-005

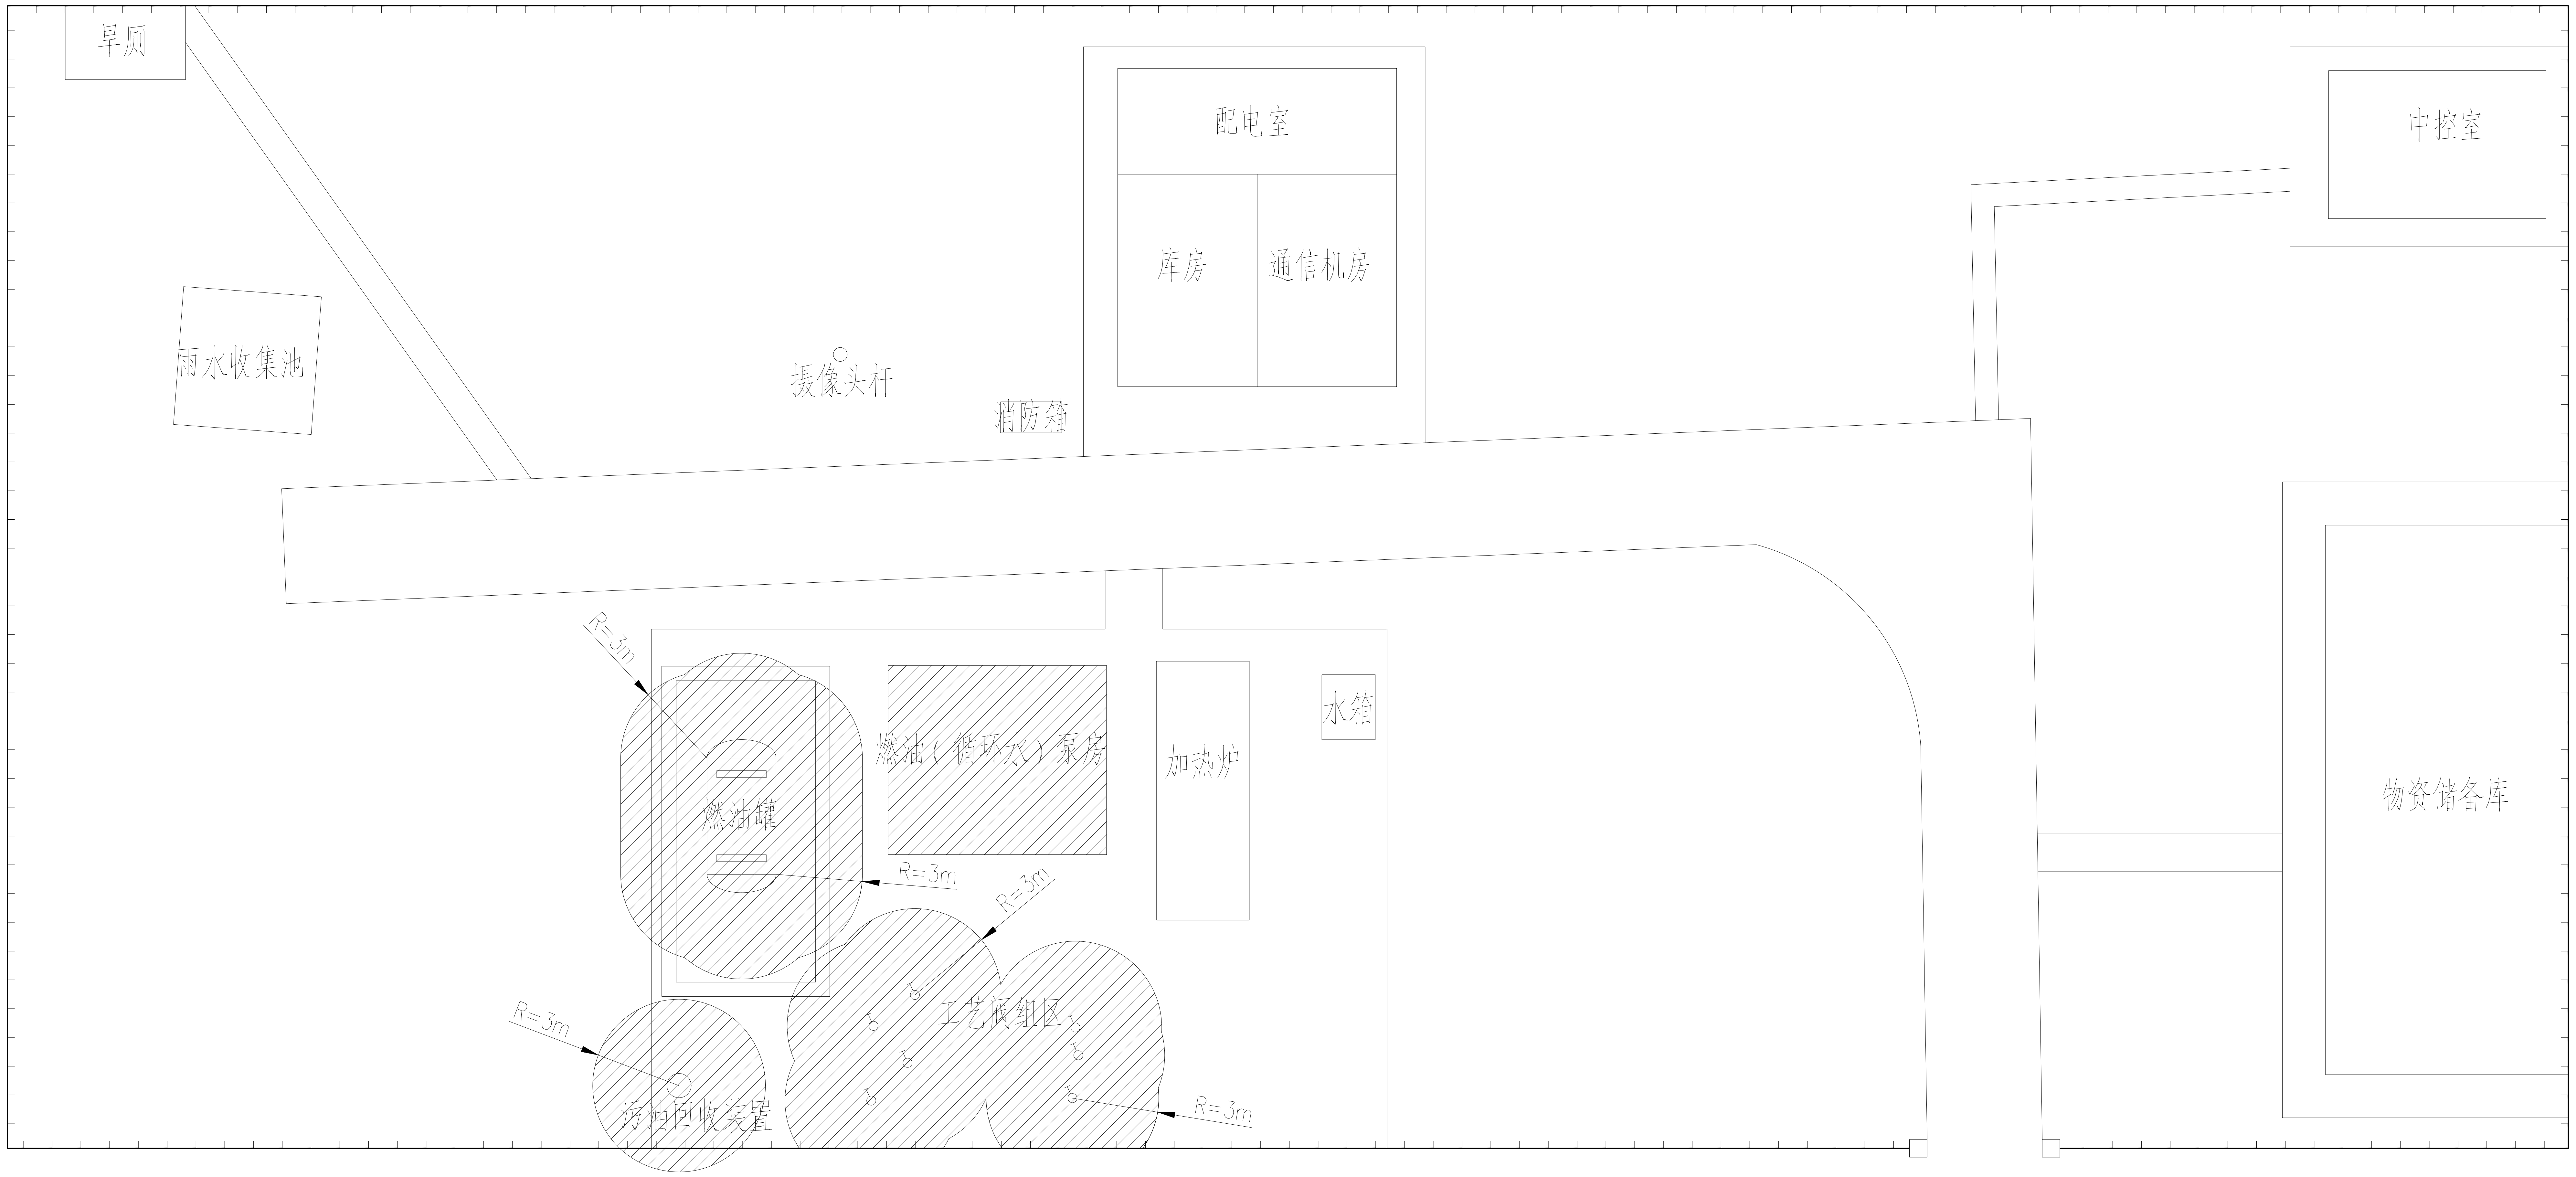

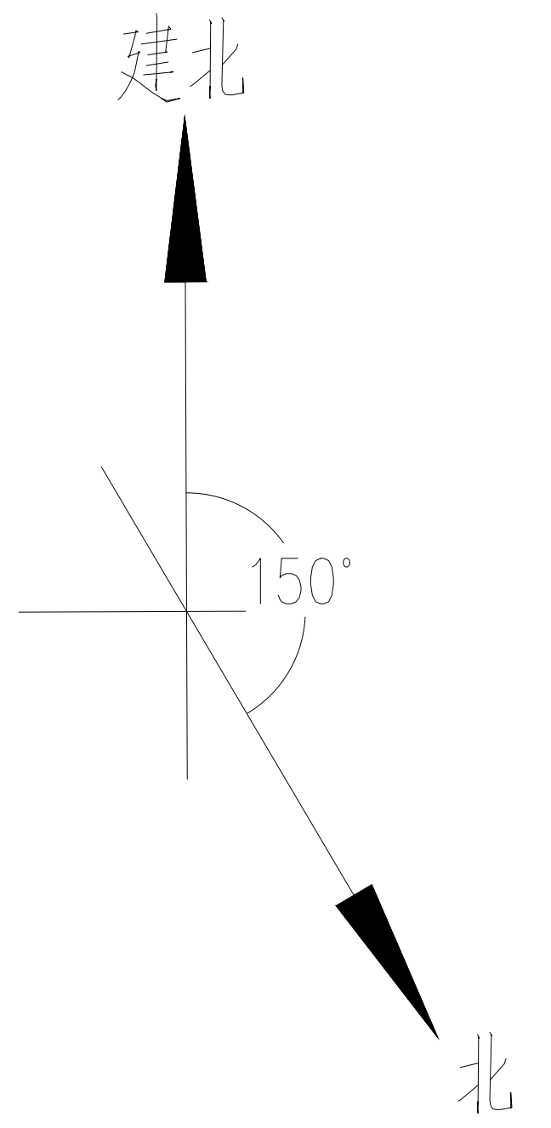

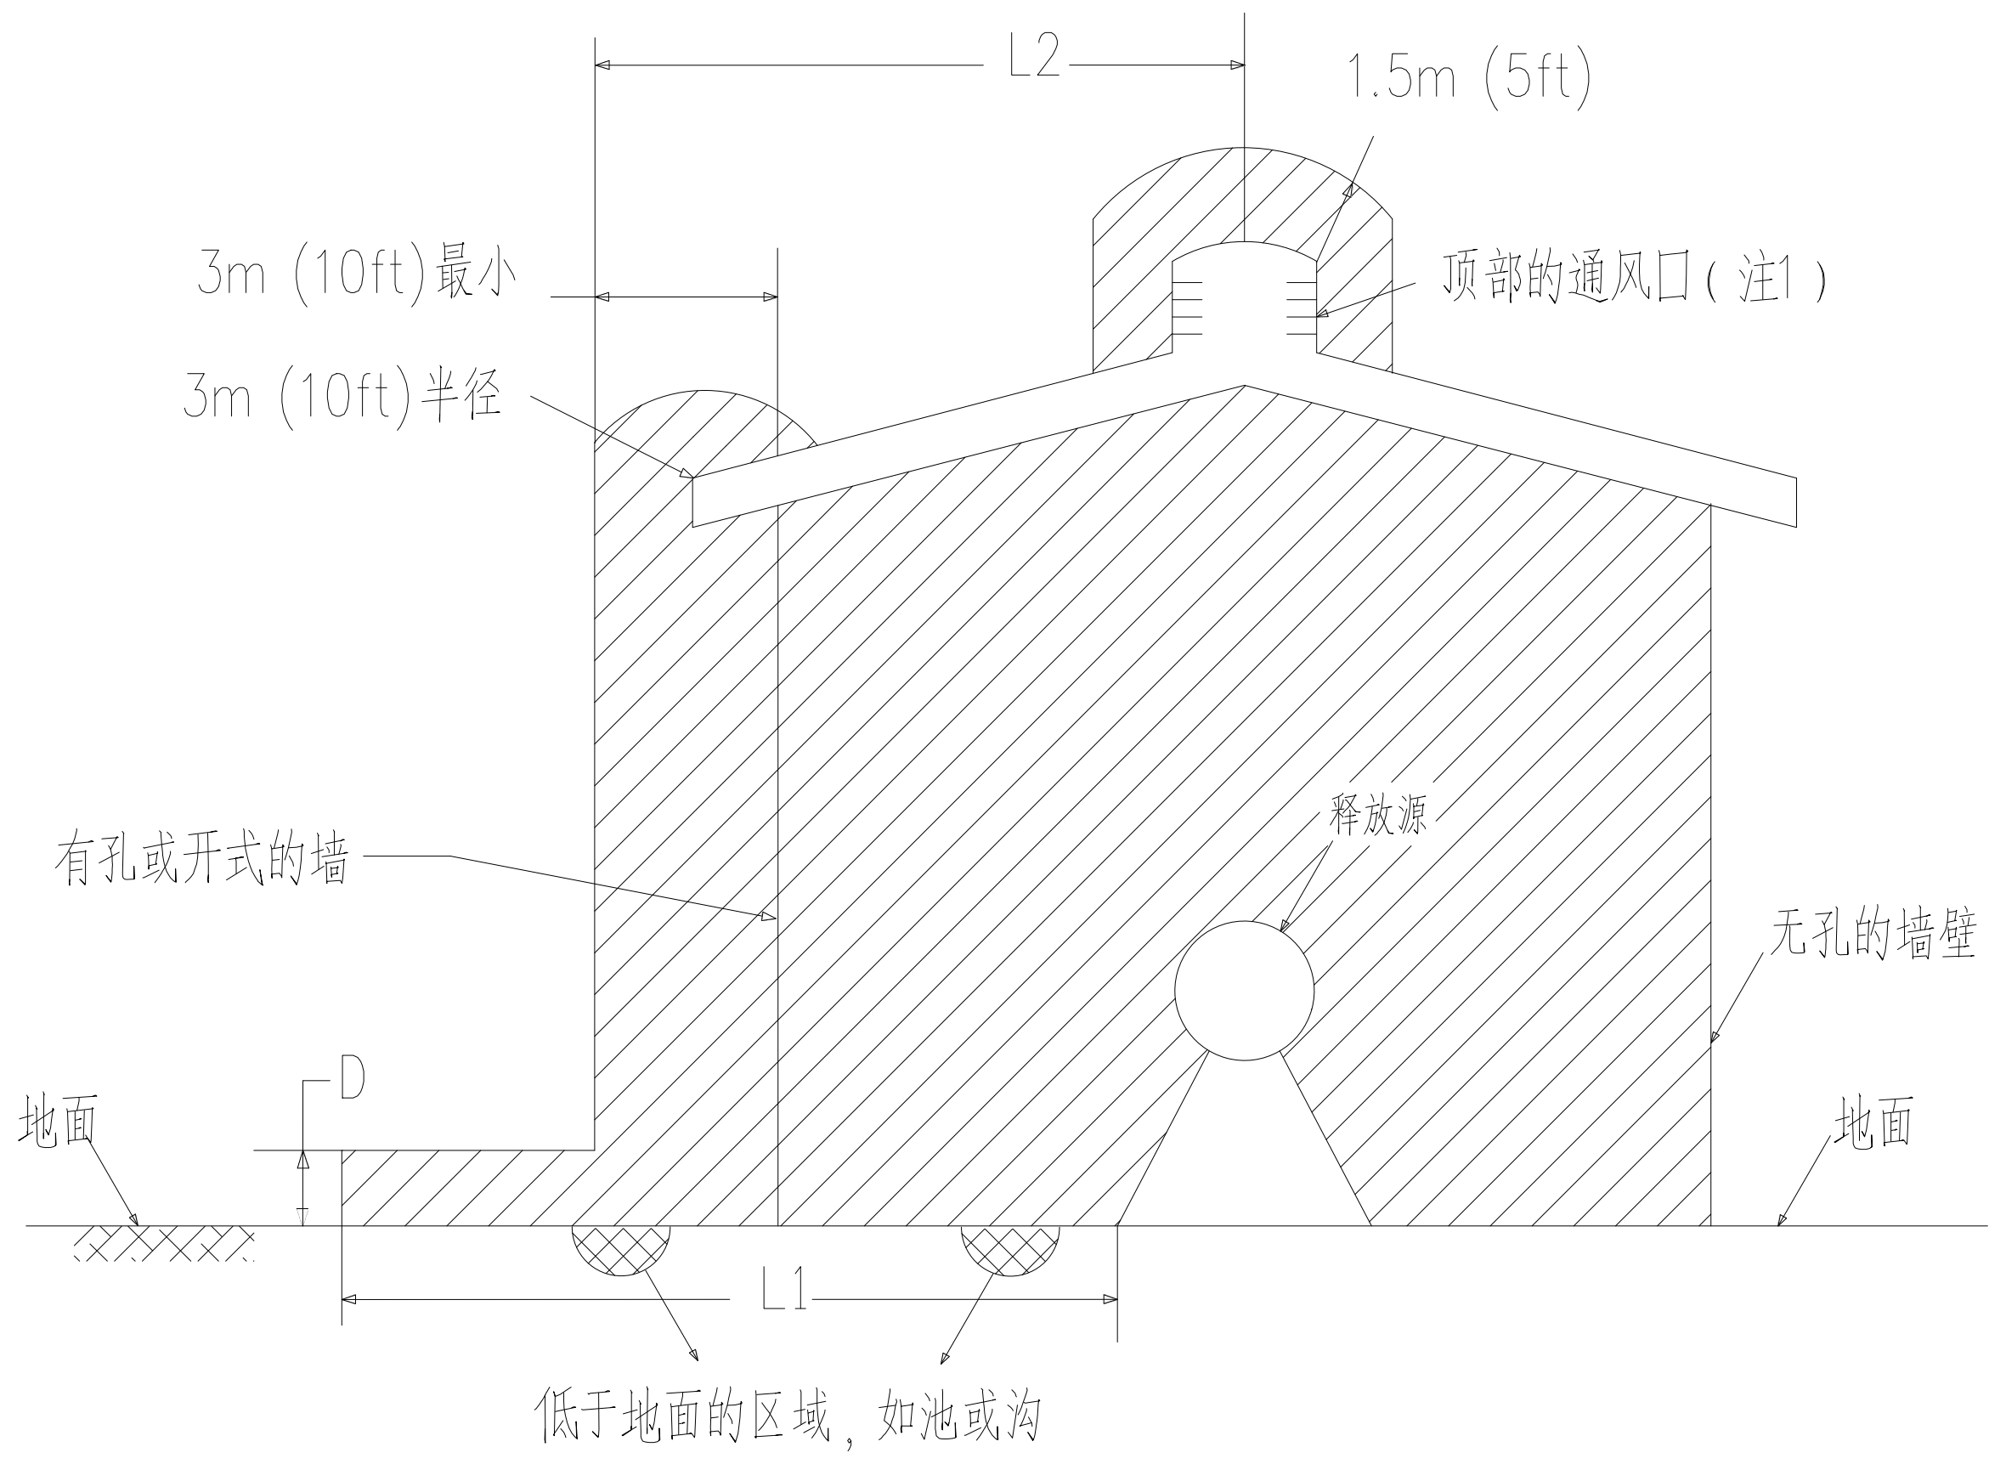

等级	距离，m（ft） L1	L2	D
1.液体表压为1900KPa（275psig）或更低	3（10）	3（10）	0.6（2）
2.液体表压高于1900KPa（275psig）（注2）	15（50）	7.5（25）	0.6（2）
3.HVL（注3）	30（100）	7.5（25）	0.6（2）

注1：通风管内部为2区，为了图面的清晰省略了剖面线。

注2：当泄漏量比较小，等级1的数据可以用于表压在1900KPa（275psig）以上操作的小泵。管线收集泵一般包括在此例之中。

注3：当泄漏量比较小，数据L1可以降低到不低于15m（50f）。

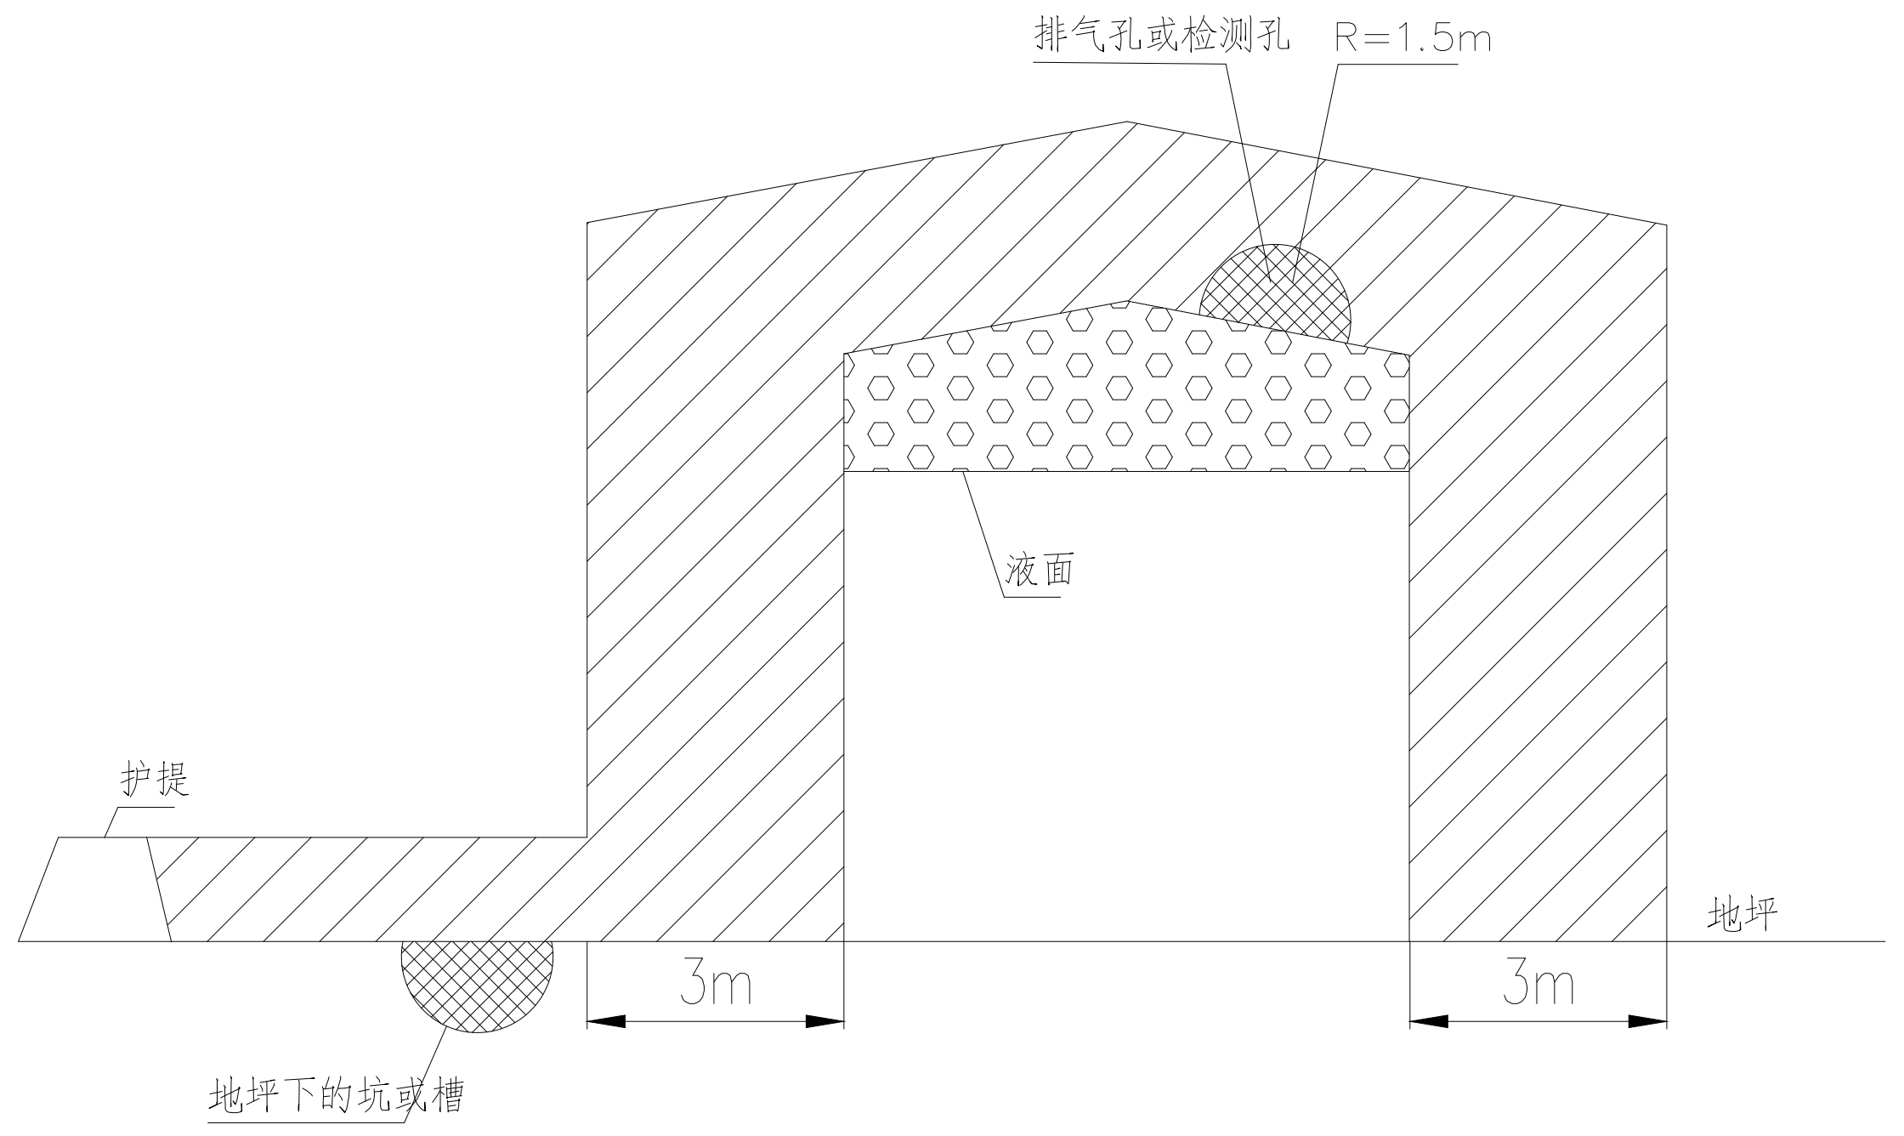

储油罐爆炸危险区域划分示意图

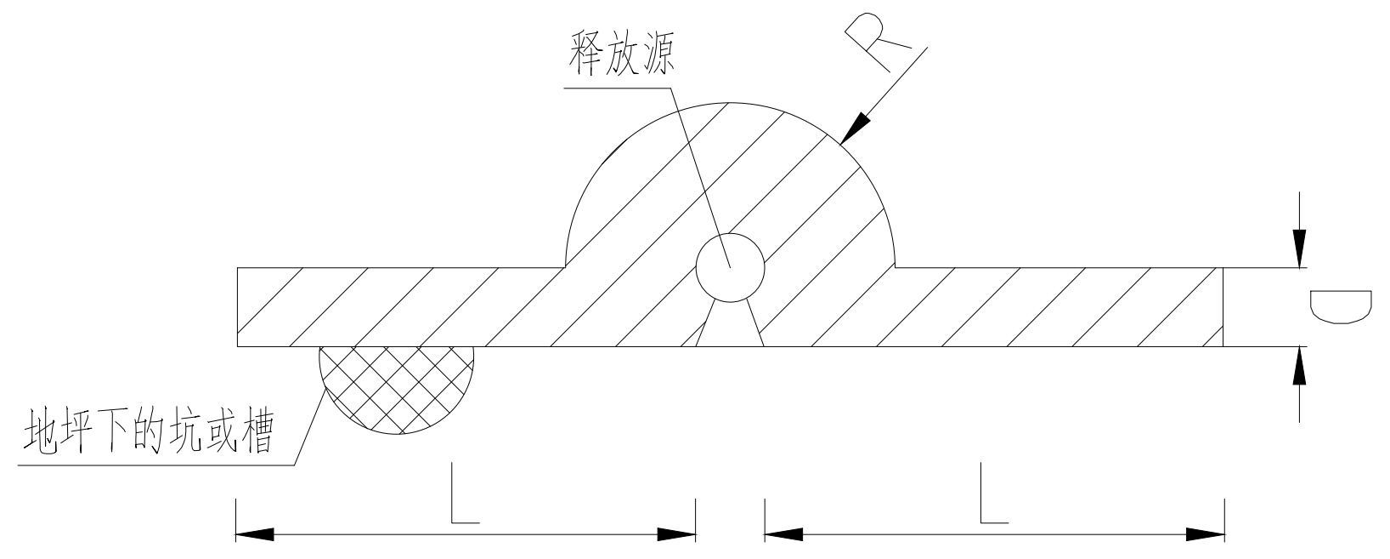

级别	L	R	D
压力≤1.9MPa	3	1	0.6
压力>1.9MPa	15	7.5	0.6
高挥发性液体	30	7.5	0.6

室外—输送易燃液体或高挥发性液体的泵或压缩机爆炸危险区域划分示意图

说明：

1）本图根据《爆炸危险环境电力装置设计规范》（GB50058-2014）、《石油设施电气设备场所I级0区、1区和2区的分类推荐作法》（SYT6671-2017）中有关规定进行绘制。

2）本次改造爆炸危险区域内地坪下的坑内应为1区，其余为2区，2区未标注范围半径均为3m。

3）释放源主要为石油，所属组别为IIA，温度组别为T3。

4）图例

图例	区域
⬡	0区
▩	1区
▨	2区

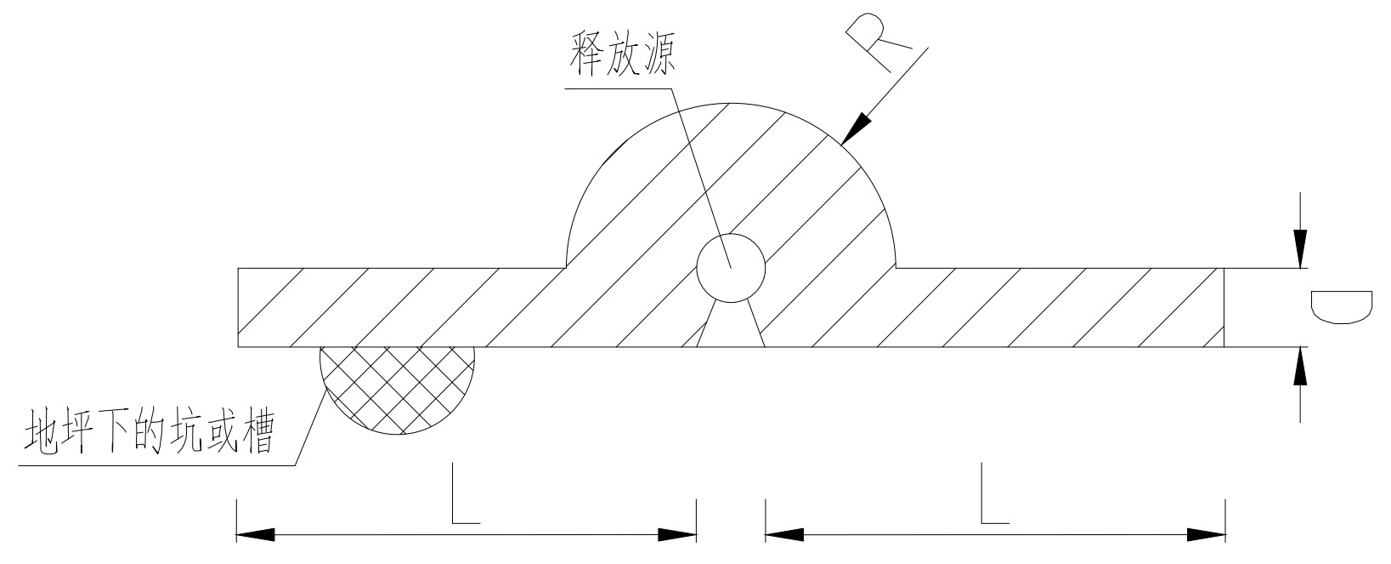

级别	L	R	D
压力≤1.9MPa	3	1	0.6
压力>1.9MPa	3	1	0.6
高挥发性液体	6	3	0.6

户外阀门、法兰爆炸危险区域划分示意图

中国石油天然气管道工程有限公司
CHINA PETROLEUM PIPELINE ENGINEERING CORPORATION
工程设计综合甲级证书编号A113A00237　工程勘察综合甲级证书编号B113A00237

制　图	葛露萍	长庆油田分公司第二输油处2026年维修工程	
设　计	葛露萍		
校　对	刘金凤	场站爆炸危险区域划分 电气部分 马营加热站爆炸危险区域划分图	
审　核	马世杰		

阶　段	施工图	文件号	DWG-0201EL01-005
比　例	1:200	项目号	DD26174
日　期	2026.04.16	版　次	0

DWG-0201EL01-006

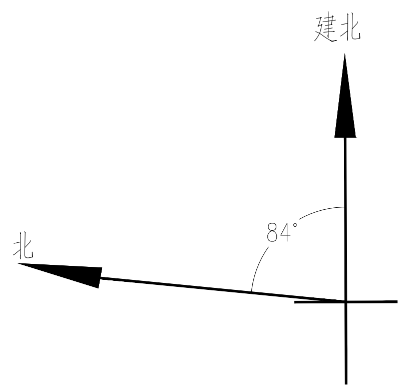

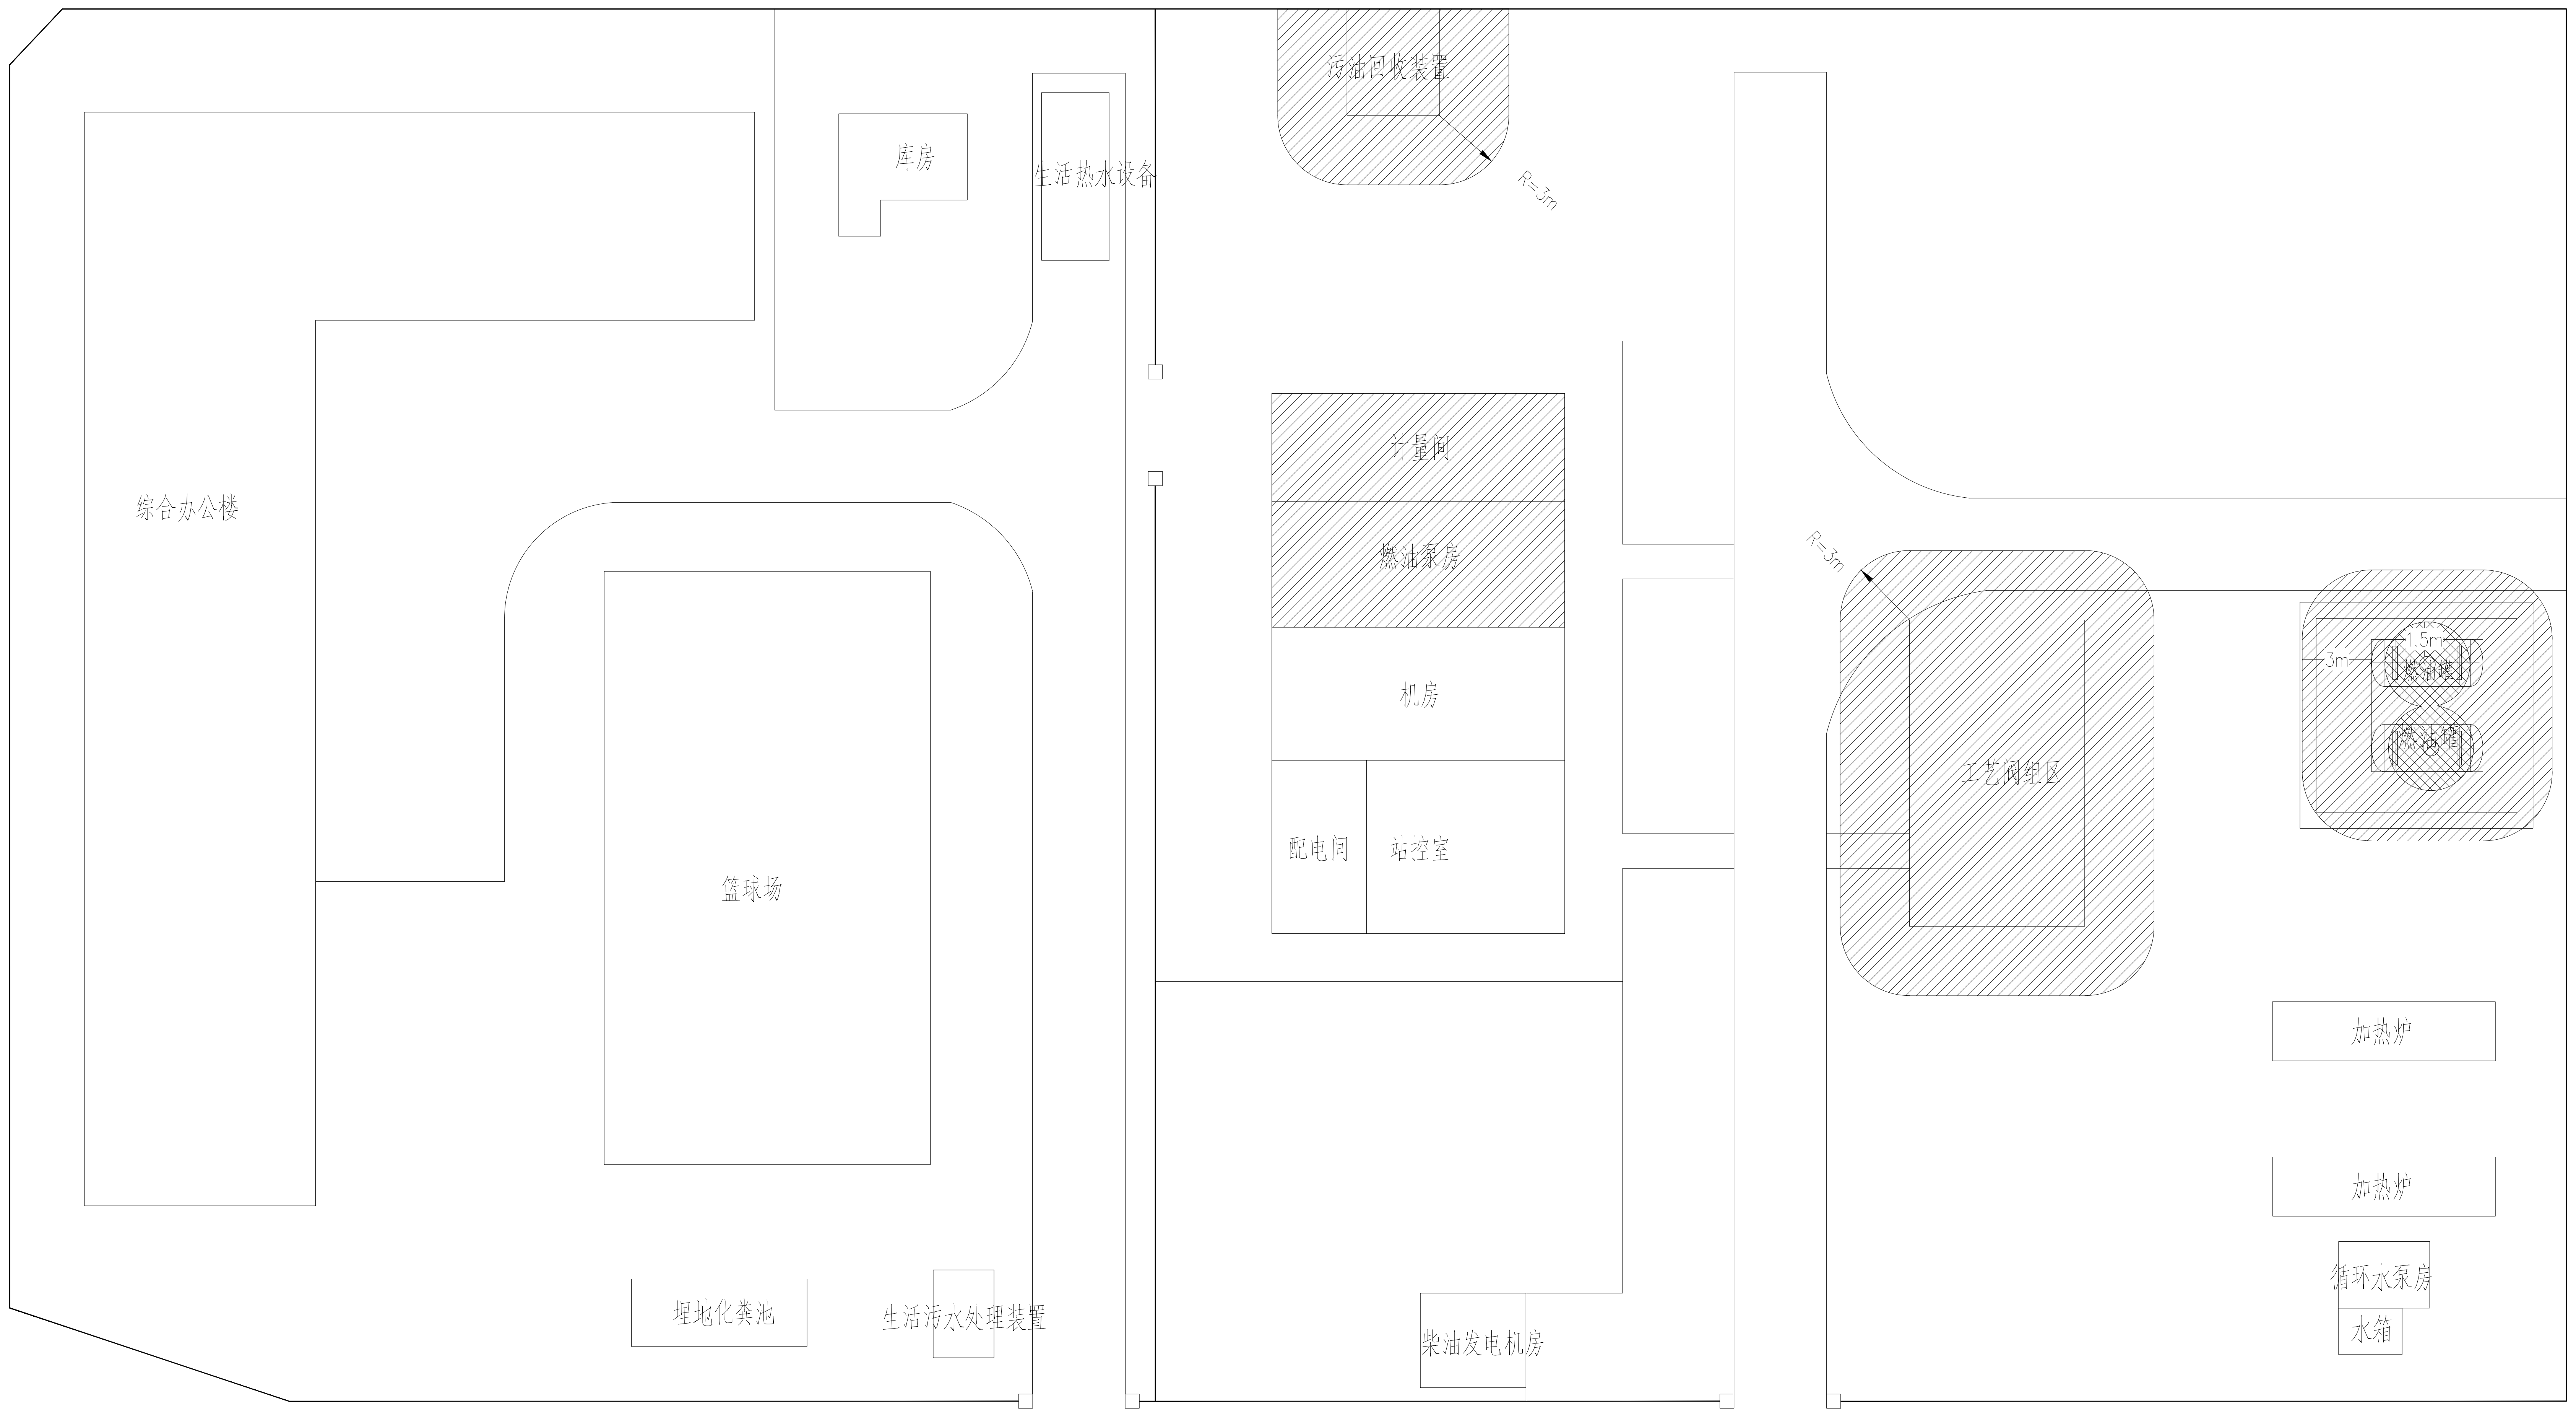

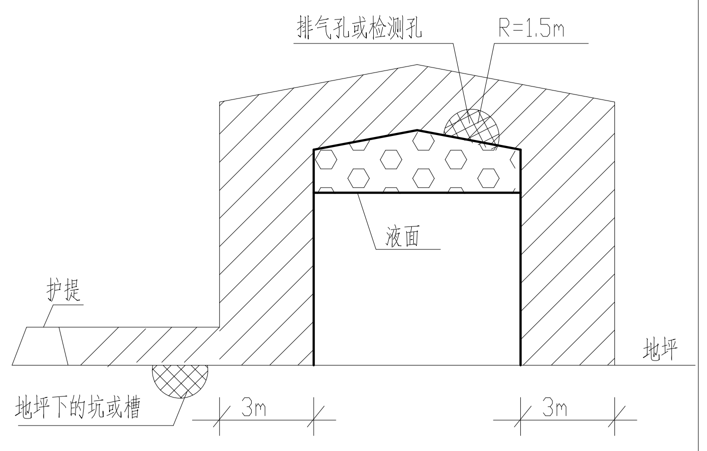

储油罐爆炸危险区域划分示意图

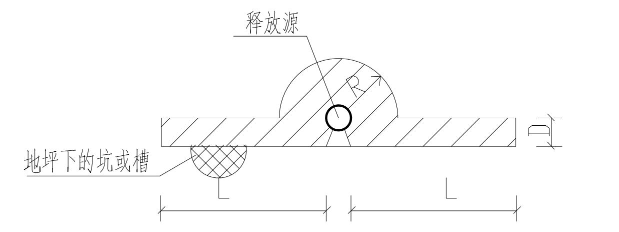

级　别	L	R	D
压力≤1.9MPa	3	1	0.6
压力 >1.9MPa	3	1	0.6
高挥发性液体	6	3	0.6

户外阀门.法兰爆炸危险区域划分示意图

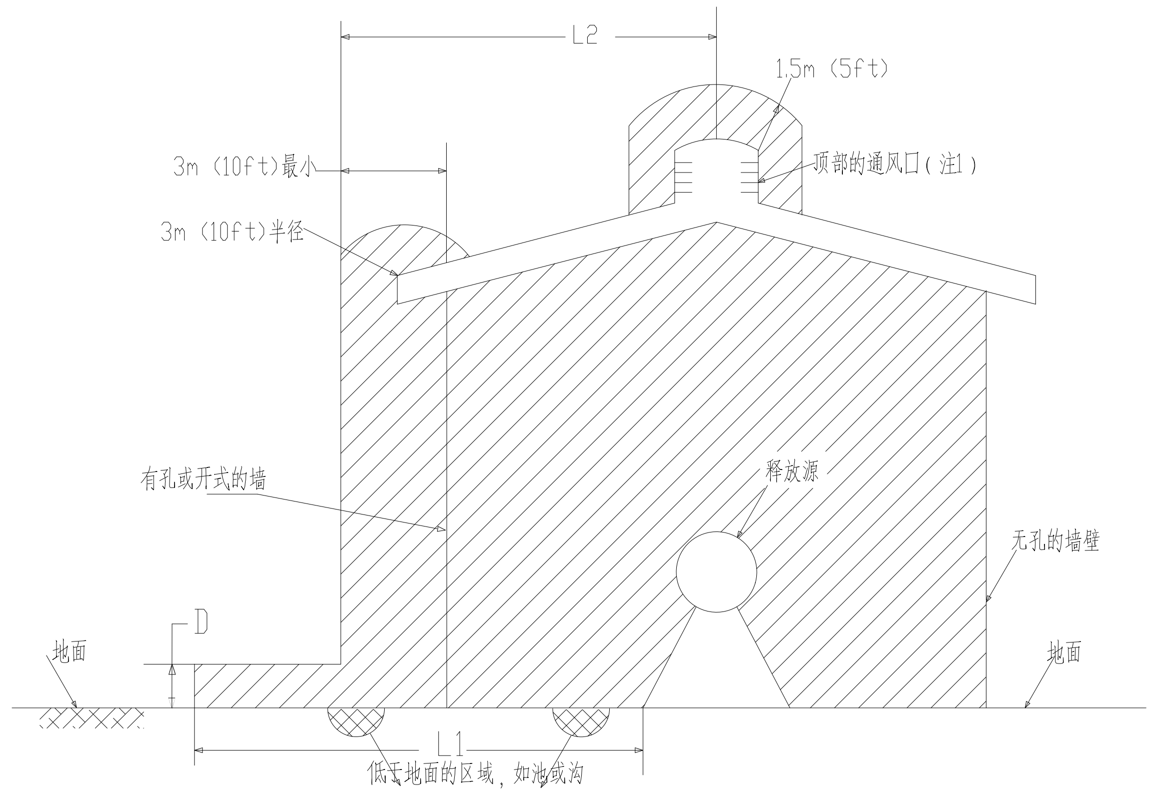

等级	距离，m(ft)		
	L1	L2	D
1.液体表压为1900KPa(275psig)或更低	3(10)	3(10)	0.6(2)
2.液体表压高于1900KPa(275psig)　(注2)	15(50)	7.5(25)	0.6(2)
3.HVL(注3)	30(100)	7.5(25)	0.6(2)

说明：

1.由于释放源位置无法确定，爆炸危险区域以工艺装置区边界进行划分。

2.依据图根据《石油设施电气设备场所Ⅰ级0区、1区和2区的分类推荐作法》(SYT 6671-2017)及《爆炸危险环境电力装置设计规范》(GB50058-2014)绘制。

3.爆炸危险区域内地坪下的坑内应为1区，其余为2区。

4.图例：

▦ 0区　▩ 1区　▨ 2区

5.释放源主要为石油，所属组别为IIA，温度组别为T3。

6.图中半径标注以米为计。

中国石油天然气管道工程有限公司

CHINA PETROLEUM PIPELINE ENGINEERING CORPORATION

工程设计综合甲级证书编号A113A00237　工程勘察综合甲级证书编号B113A00237

制　图	刘金风	长庆油田分公司第二输油处2026年维修工程			
设　计	刘金风	场站爆炸危险区域划分 电气部分 乔川加温站爆炸危险区域划分图			
校　对	葛露萍				
审　核	马红志				
		阶　段	施工图	文件号	DWG-0201EL01-006
		比　例	1:250	项目号	DD26174
		日　期	2026.4.16	版　次	0

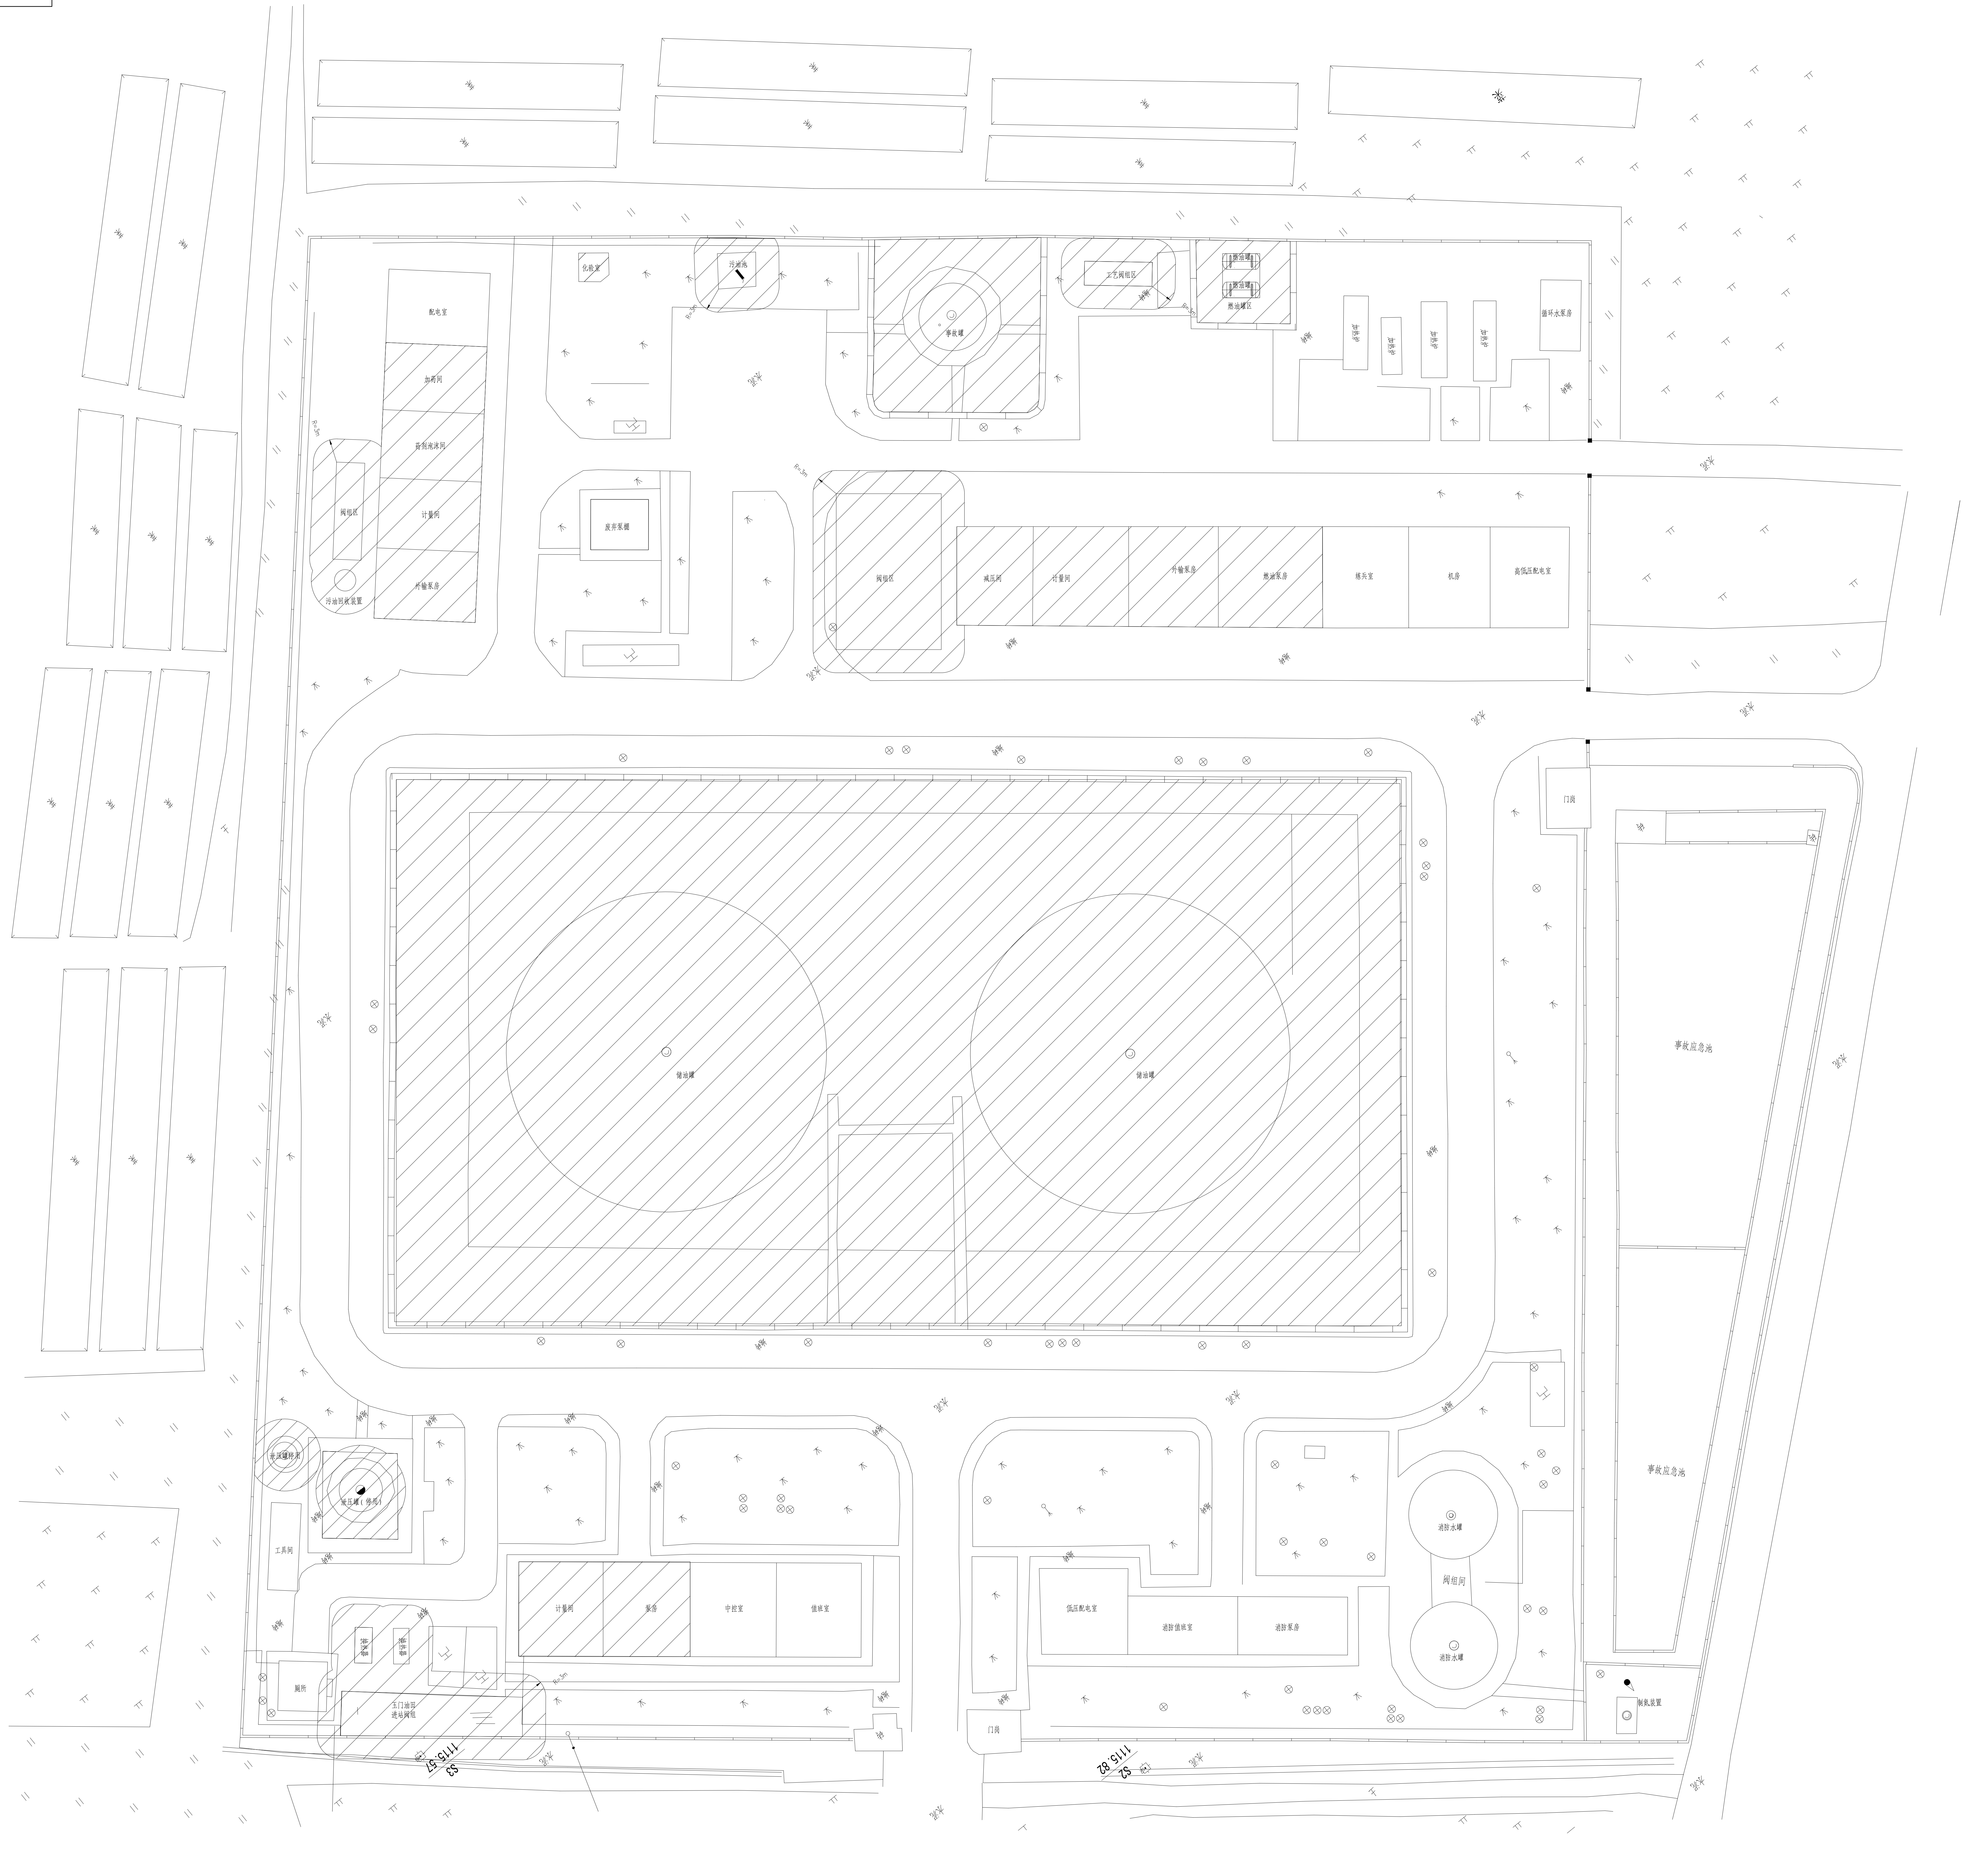

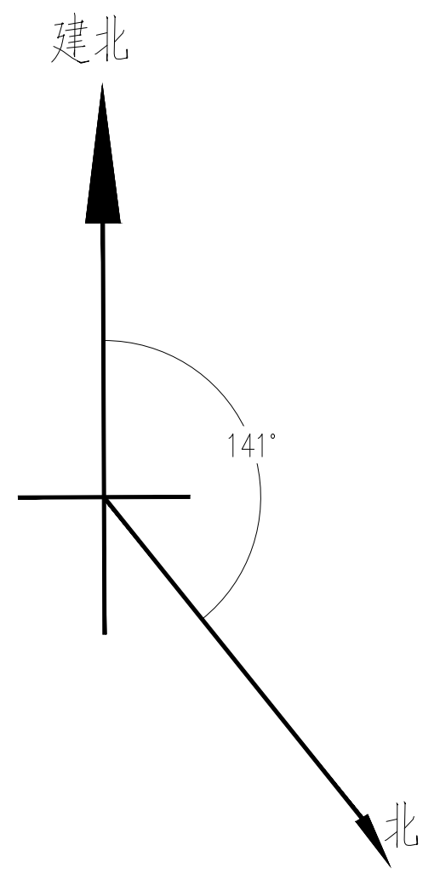

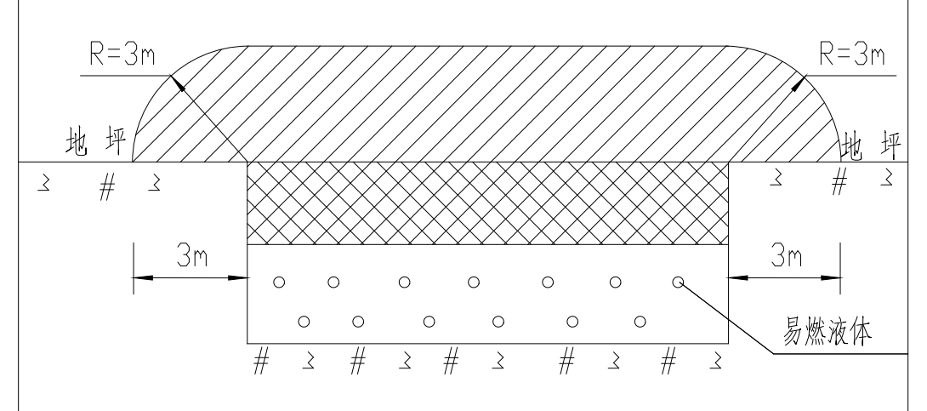

污油池爆炸危险区域划分示意图

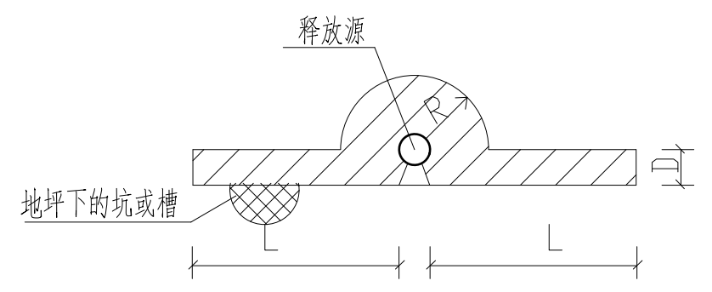

级 别	L	R	D
压力≤1.9MPa	3	1	0.6
压力＞1.9MPa	3	1	0.6
高挥发性液体	6	3	0.6

户外阀门.法兰爆炸危险区域划分示意图

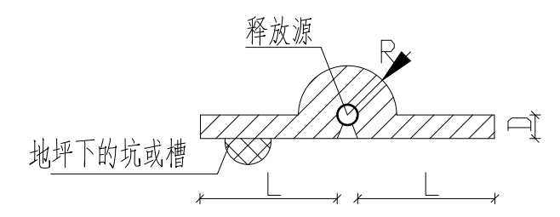

级 别	L	R	D
压力≤1.9MPa	3	1	0.6
压力>1.9MPa	15	7.5	0.6
高挥发性液体	30	7.5	0.6

室外—输送易燃液体或高挥发性液体的压缩机或泵爆炸危险区域划分示意图

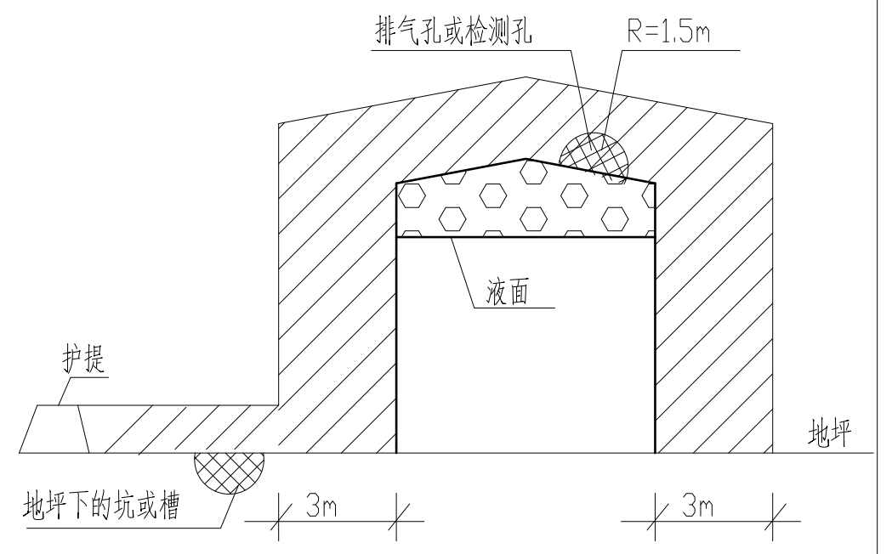

储油罐爆炸危险区域划分示意图

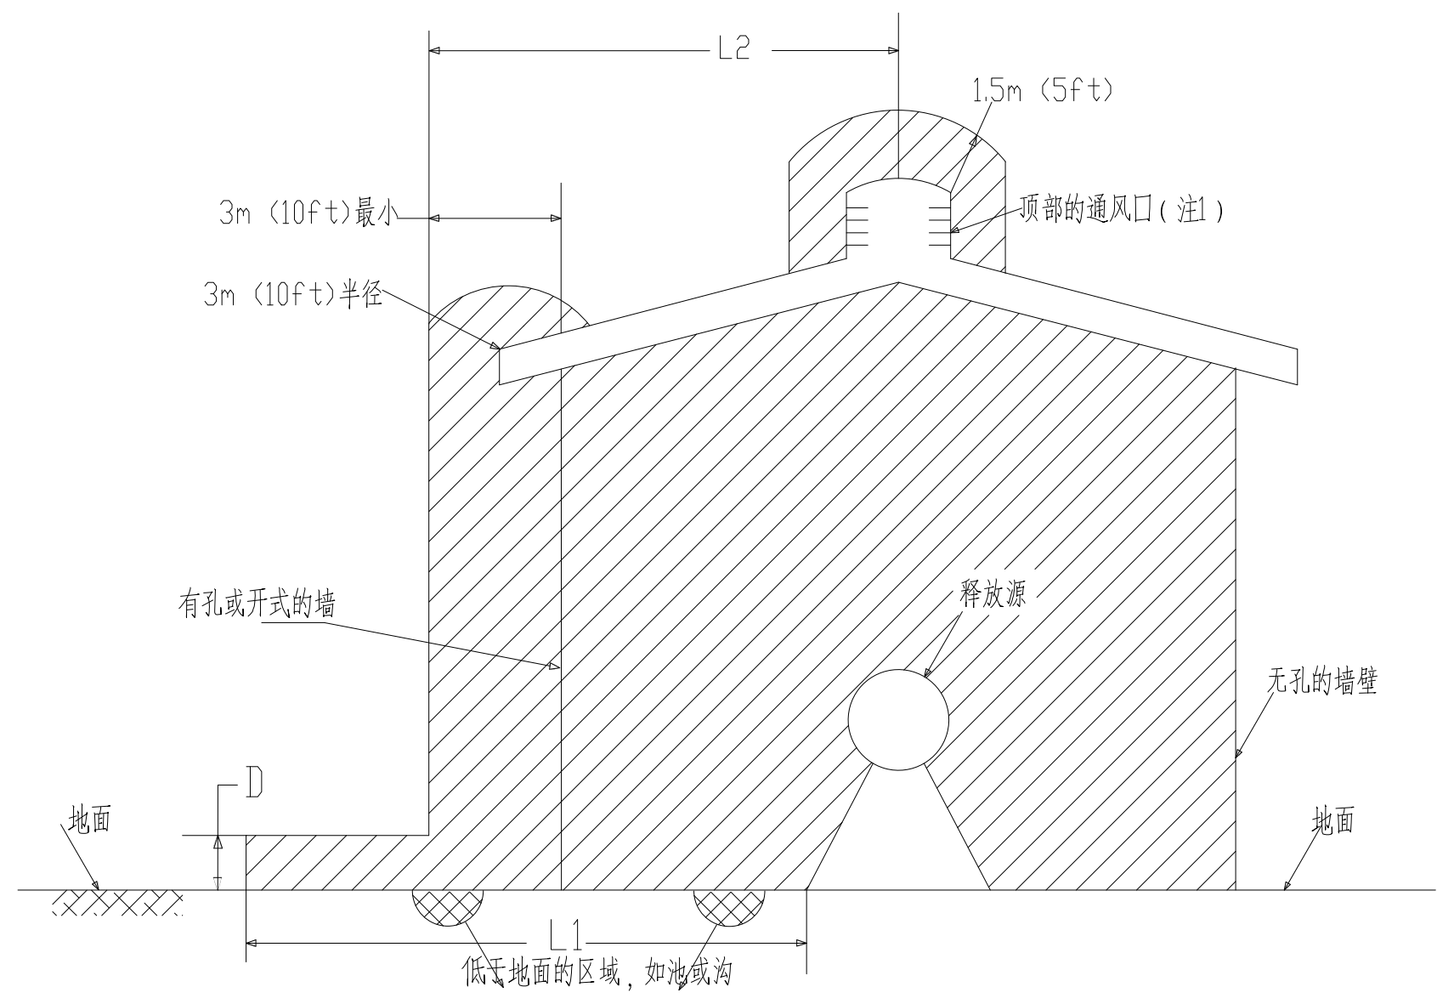

<table>
<tr><th rowspan="2">等级</th><th colspan="3">距离，m（ft）</th></tr>
<tr><th>L1</th><th>L2</th><th>D</th></tr>
<tr><td>1.液体表压为1900KPa（275psig）或更低</td><td>3（10）</td><td>3（10）</td><td>0.6（2）</td></tr>
<tr><td>2.液体表压高于1900KPa（275psig） （注2）</td><td>15（50）</td><td>7.5（25）</td><td>0.6（2）</td></tr>
<tr><td>3.HVL（注3）</td><td>30（100）</td><td>7.5（25）</td><td>0.6（2）</td></tr>
</table>

说明：

1.由于释放源位置无法确定，爆炸危险区域以工艺装置区边界进行划分。

2.依据图根据《石油设施电气设备场所Ⅰ级0区、1区和2区的分类推荐作法》(SYT 6671-2017)及《爆炸危险环境电力装置设计规范》（GB50058-2014）绘制。

3.爆炸危险区域内地坪下的坑内应为1区,其余为2区。

4.图例: 0区 1区 2区

5.释放源主要为石油，所属组别为IIA，温度组别为T3。

6.图中半径标注以米为计。

中国石油天然气管道工程有限公司
CHINA PETROLEUM PIPELINE ENGINEERING CORPORATION
工程设计综合甲级证书编号A113A00237 工程勘察综合甲级证书编号B113A00237

制 图	刘金凤	长庆油田分公司第二输油处2026年维修工程			
设 计	刘金凤				
校 对	聂露萍	场站爆炸危险区域划分 电气部分 曲子输油站爆炸危险区域划分图			
审 核					
		阶 段	施工图	文件号	DWG-0201EL01-007
		比 例	1:300	项目号	DD26174
		日 期	2026.4.16	版 次	0

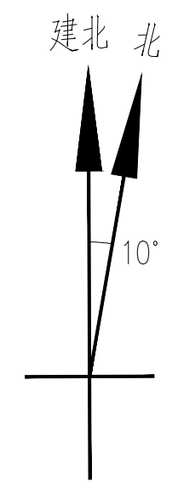

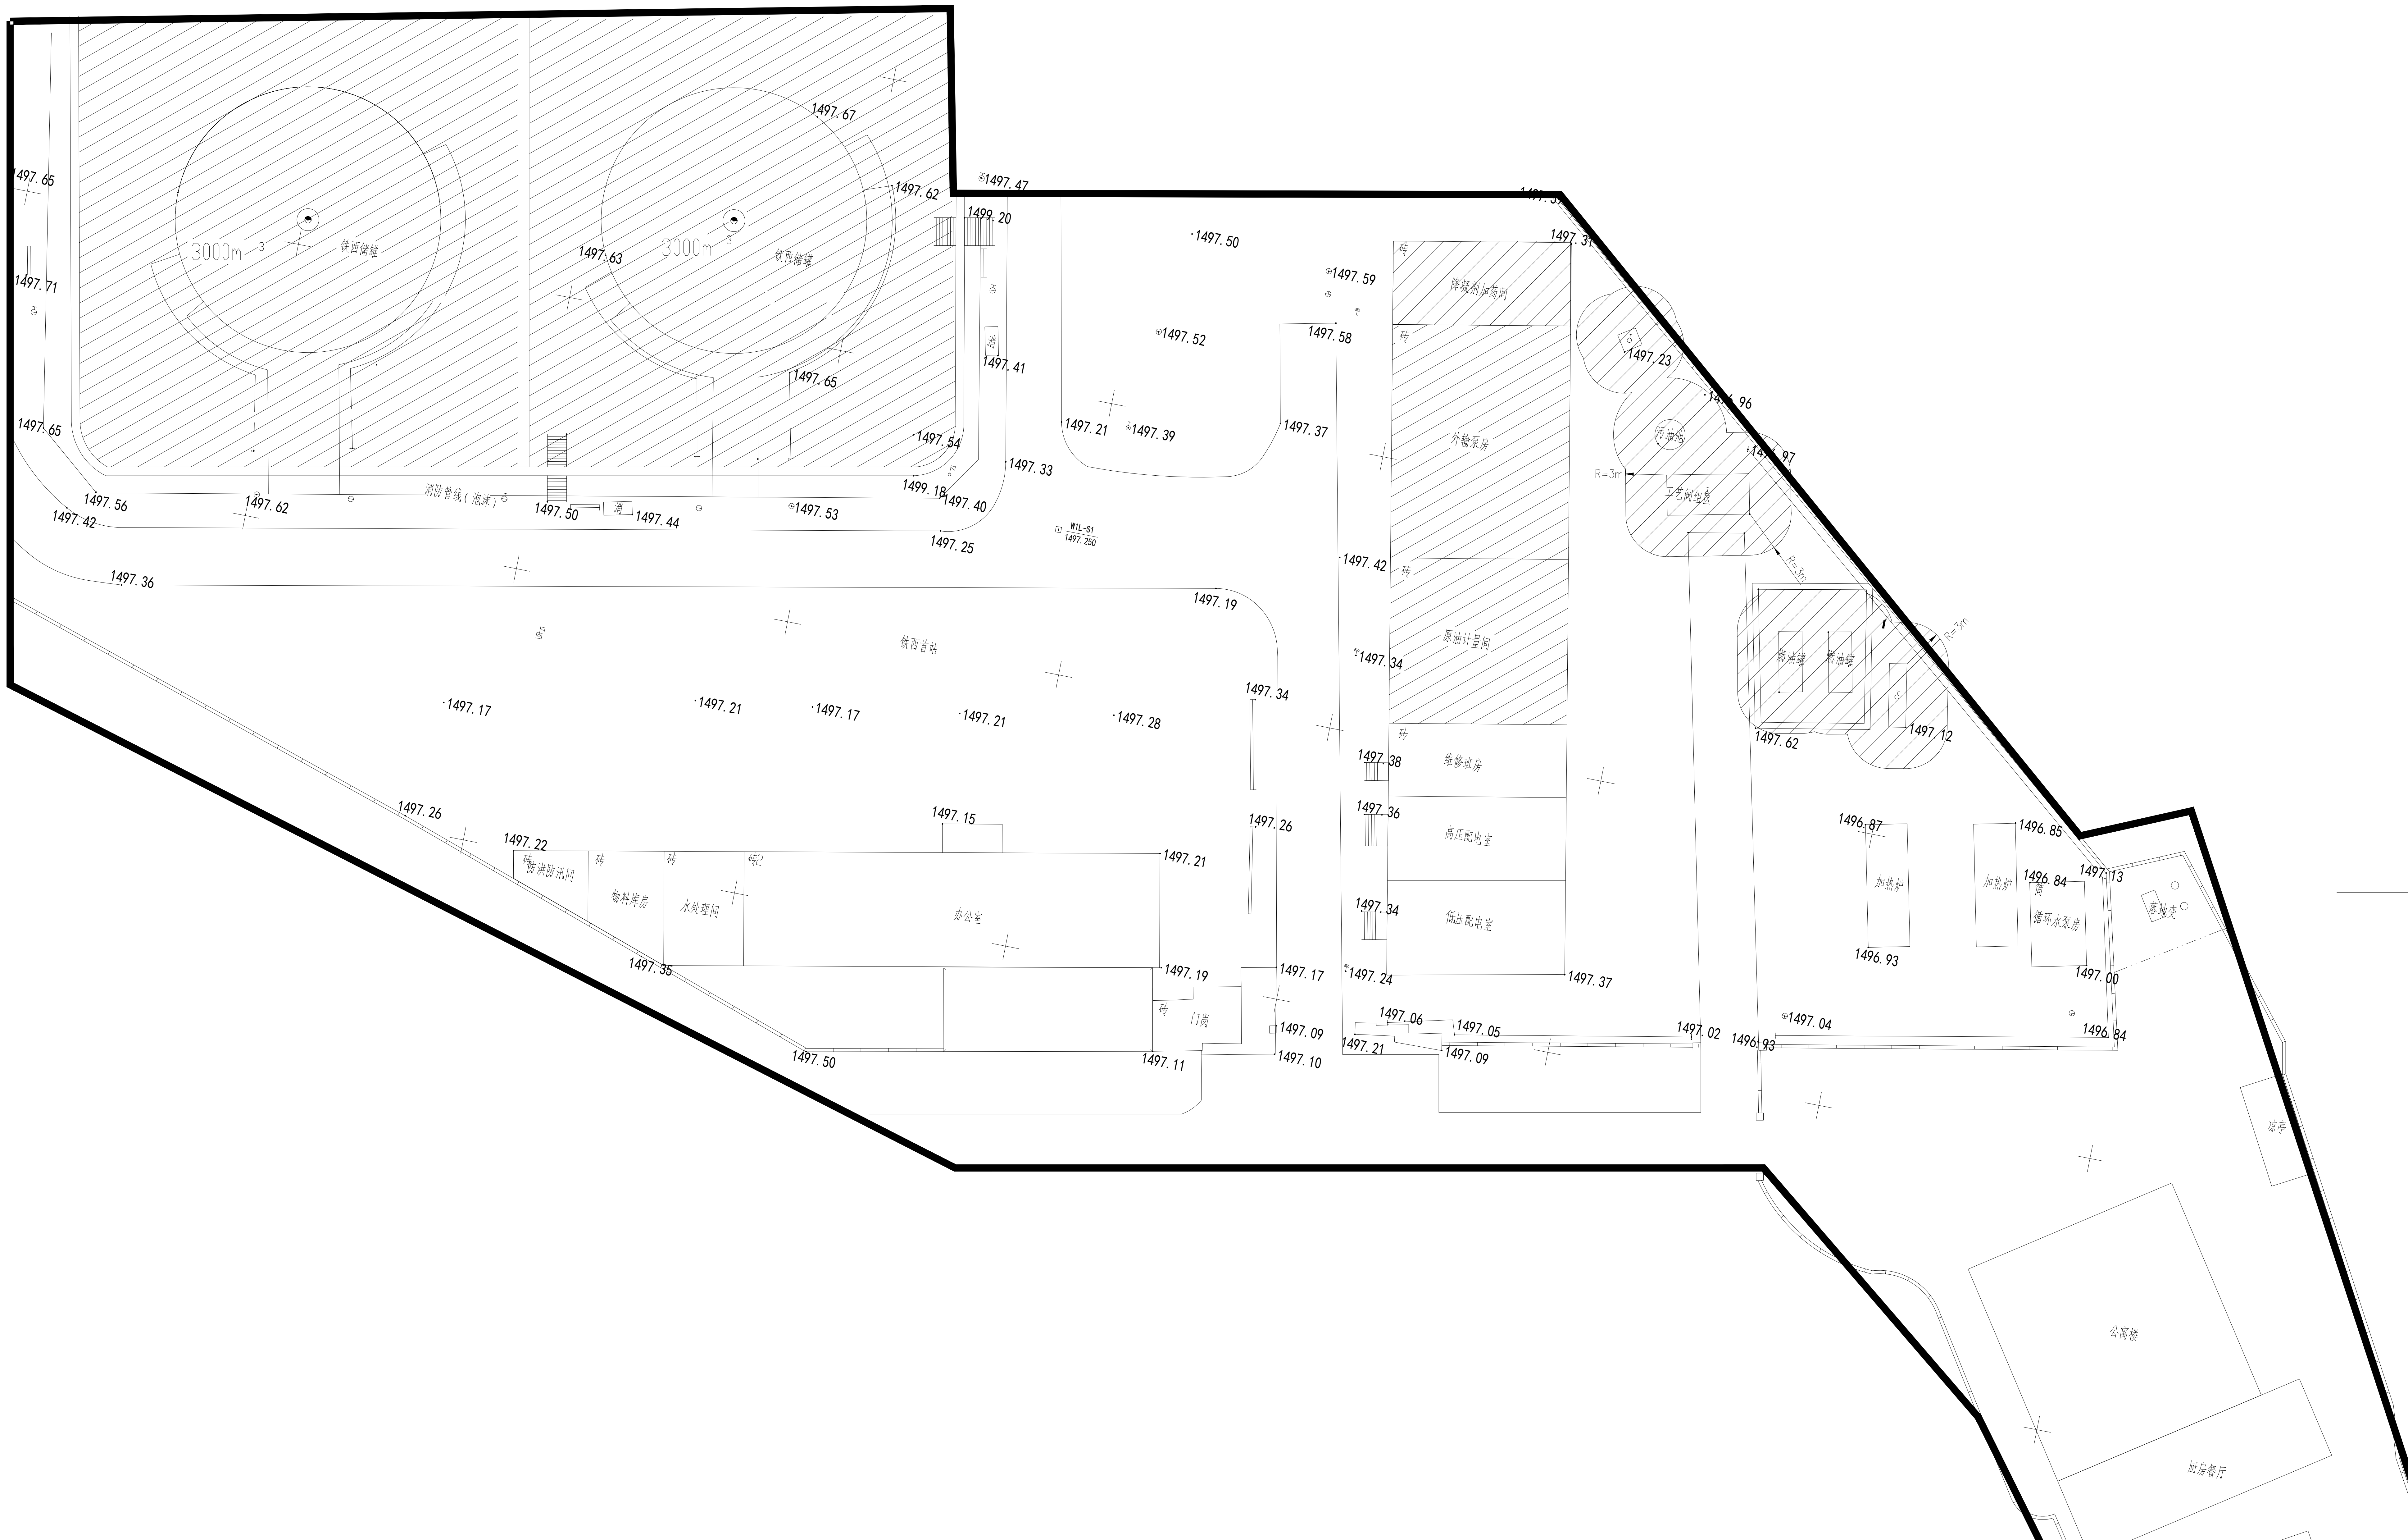

说明：

1. 由于释放源位置无法确定，爆炸危险区域以工艺装置区边界进行划分。
2. 依据图根据《石油设施电气设备场所Ⅰ级0区、1区和2区的分类推荐作法》(SYT 6671-2017)及《爆炸危险环境电力装置设计规范》(GB50058-2014)绘制。
3. 爆炸危险区域内地坪下的坑内应为1区，其余为2区。
4. 图例：

▦ 0区　▩ 1区　▨ 2区

5. 释放源主要为石油，所属组别为IIA，温度组别为T3。
6. 图中半径标注以米为计。

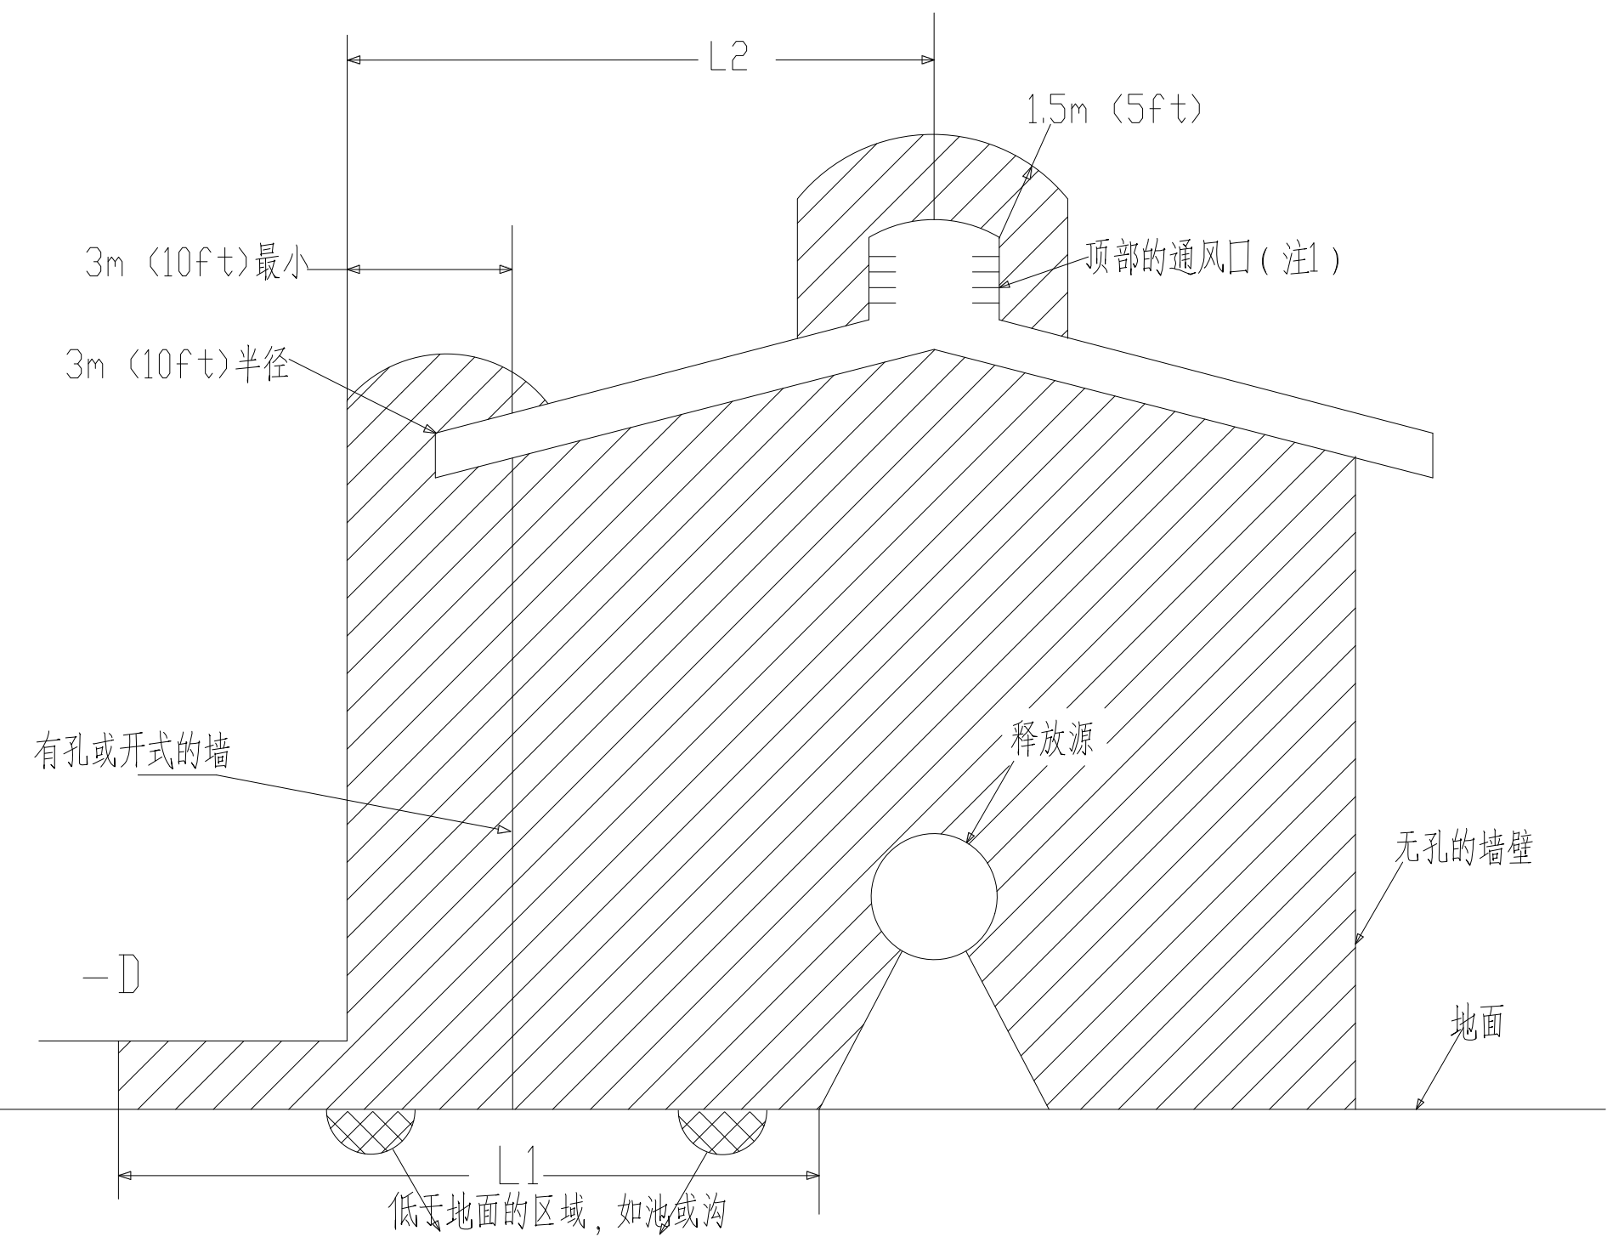

等级	距离，m(ft)		
	L1	L2	D
1.液体表压为1900KPa(275psig)或更低	3(10)	3(10)	0.6(2)
2.液体表压高于1900KPa(275psig) (注2)	15(50)	7.5(25)	0.6(2)
3.HVL(注3)	30(100)	7.5(25)	0.6(2)

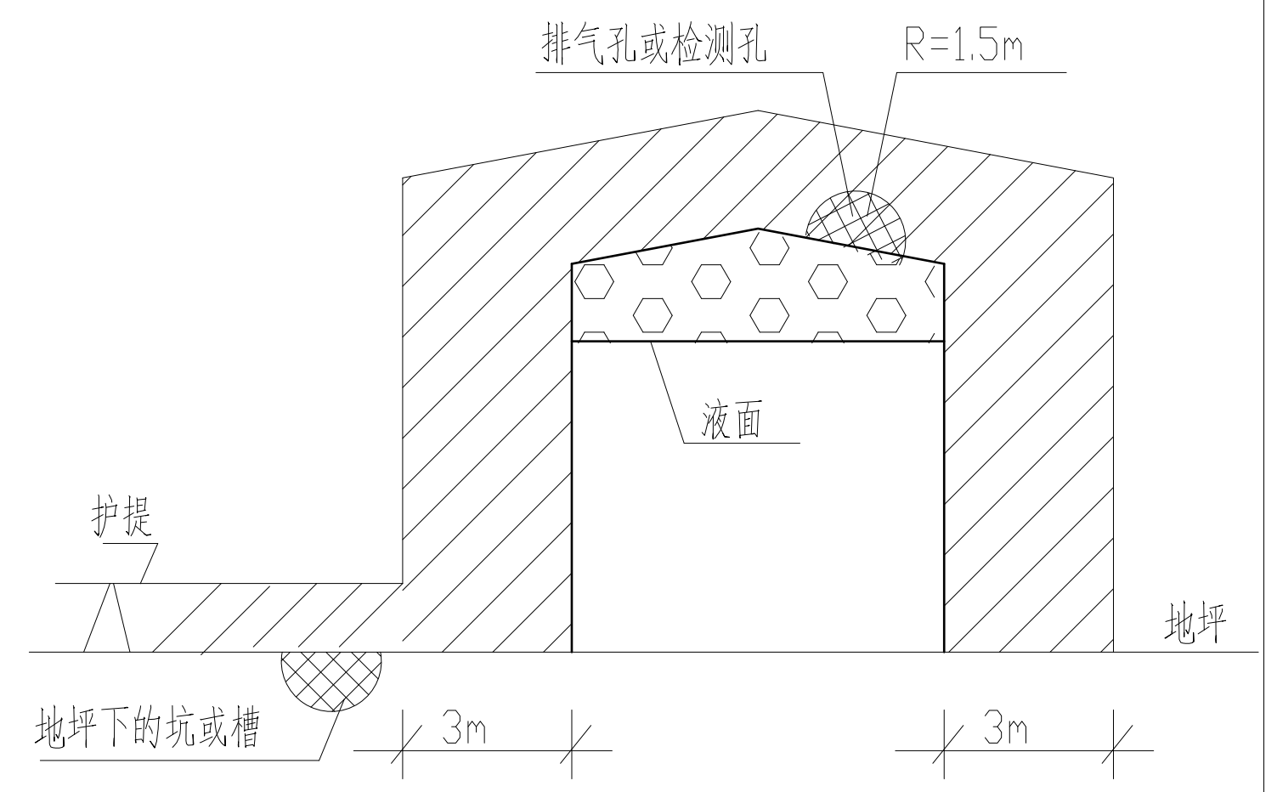

储油罐爆炸危险区域划分示意图

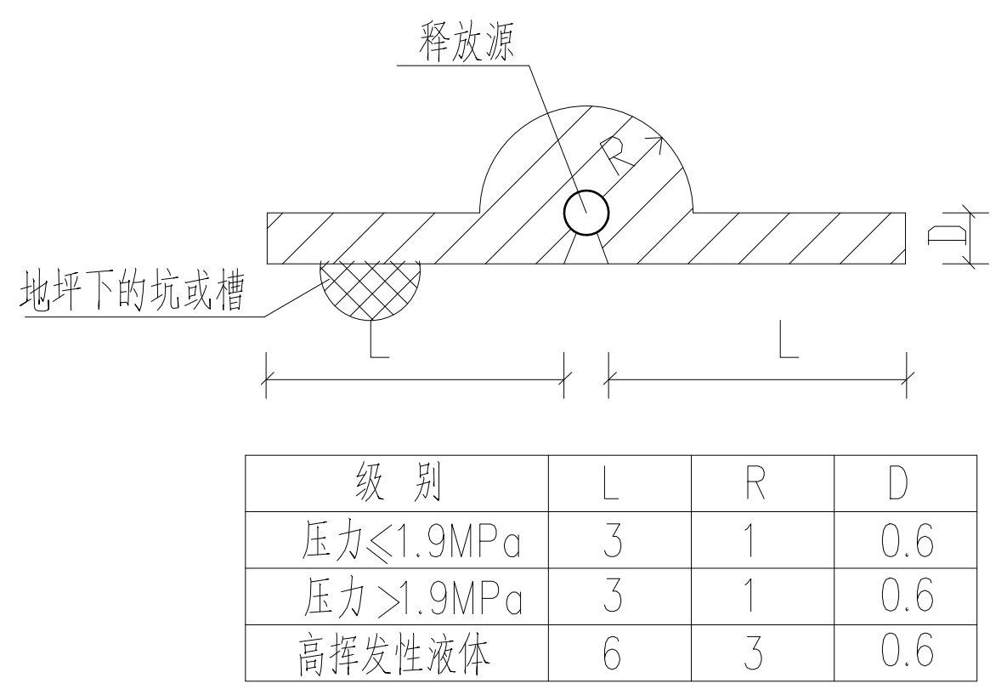

级　别	L	R	D
压力≤1.9MPa	3	1	0.6
压力>1.9MPa	3	1	0.6
高挥发性液体	6	3	0.6

户外阀门.法兰爆炸危险区域划分示意图

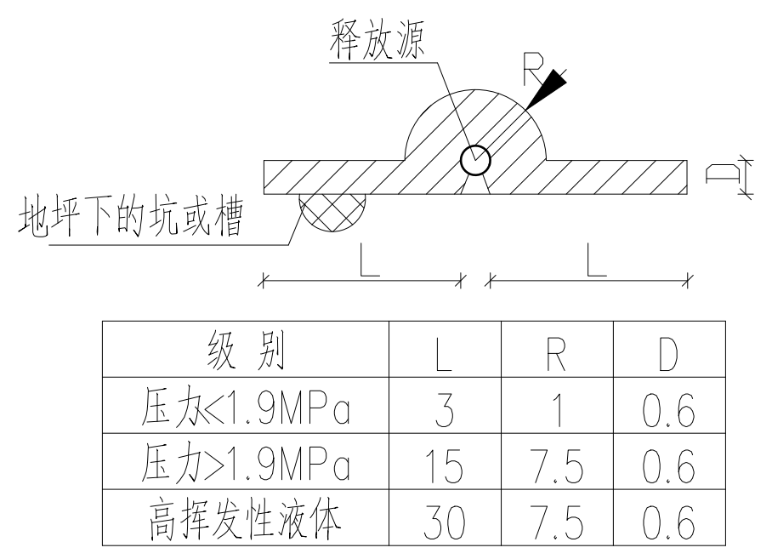

级　别	L	R	D
压力<1.9MPa	3	1	0.6
压力>1.9MPa	15	7.5	0.6
高挥发性液体	30	7.5	0.6

室外—输送易燃液体或高挥发性液体的
压缩机或泵爆炸危险区域划分示意图

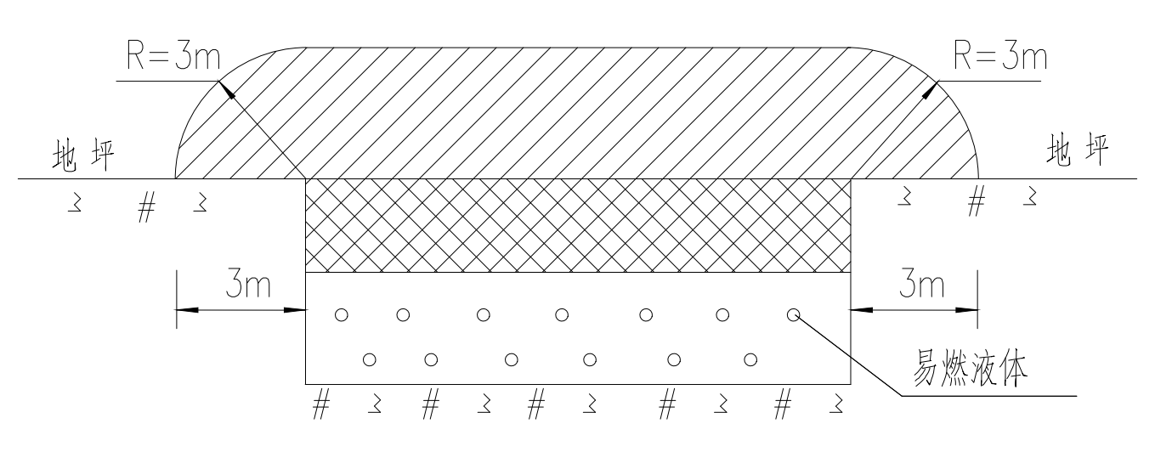

污油池爆炸危险区域划分示意图

中国石油天然气管道工程有限公司
CHINA PETROLEUM PIPELINE ENGINEERING CORPORATION
工程设计综合甲级证书编号A113A00237　工程勘察综合甲级证书编号B113A00237

制　图	杨麟淇	长庆油田分公司第二输油处2026年维修工程
设　计	杨麟淇	
校　对	刘金凤	场站爆炸危险区域划分 电气部分 铁西首站爆炸危险区域划分图
审　核		

阶　段	施工图	文件号	DWG-0201EL01-008
比　例	1:200	项目号	DD26174
日　期	2026.4.16	版　次	0