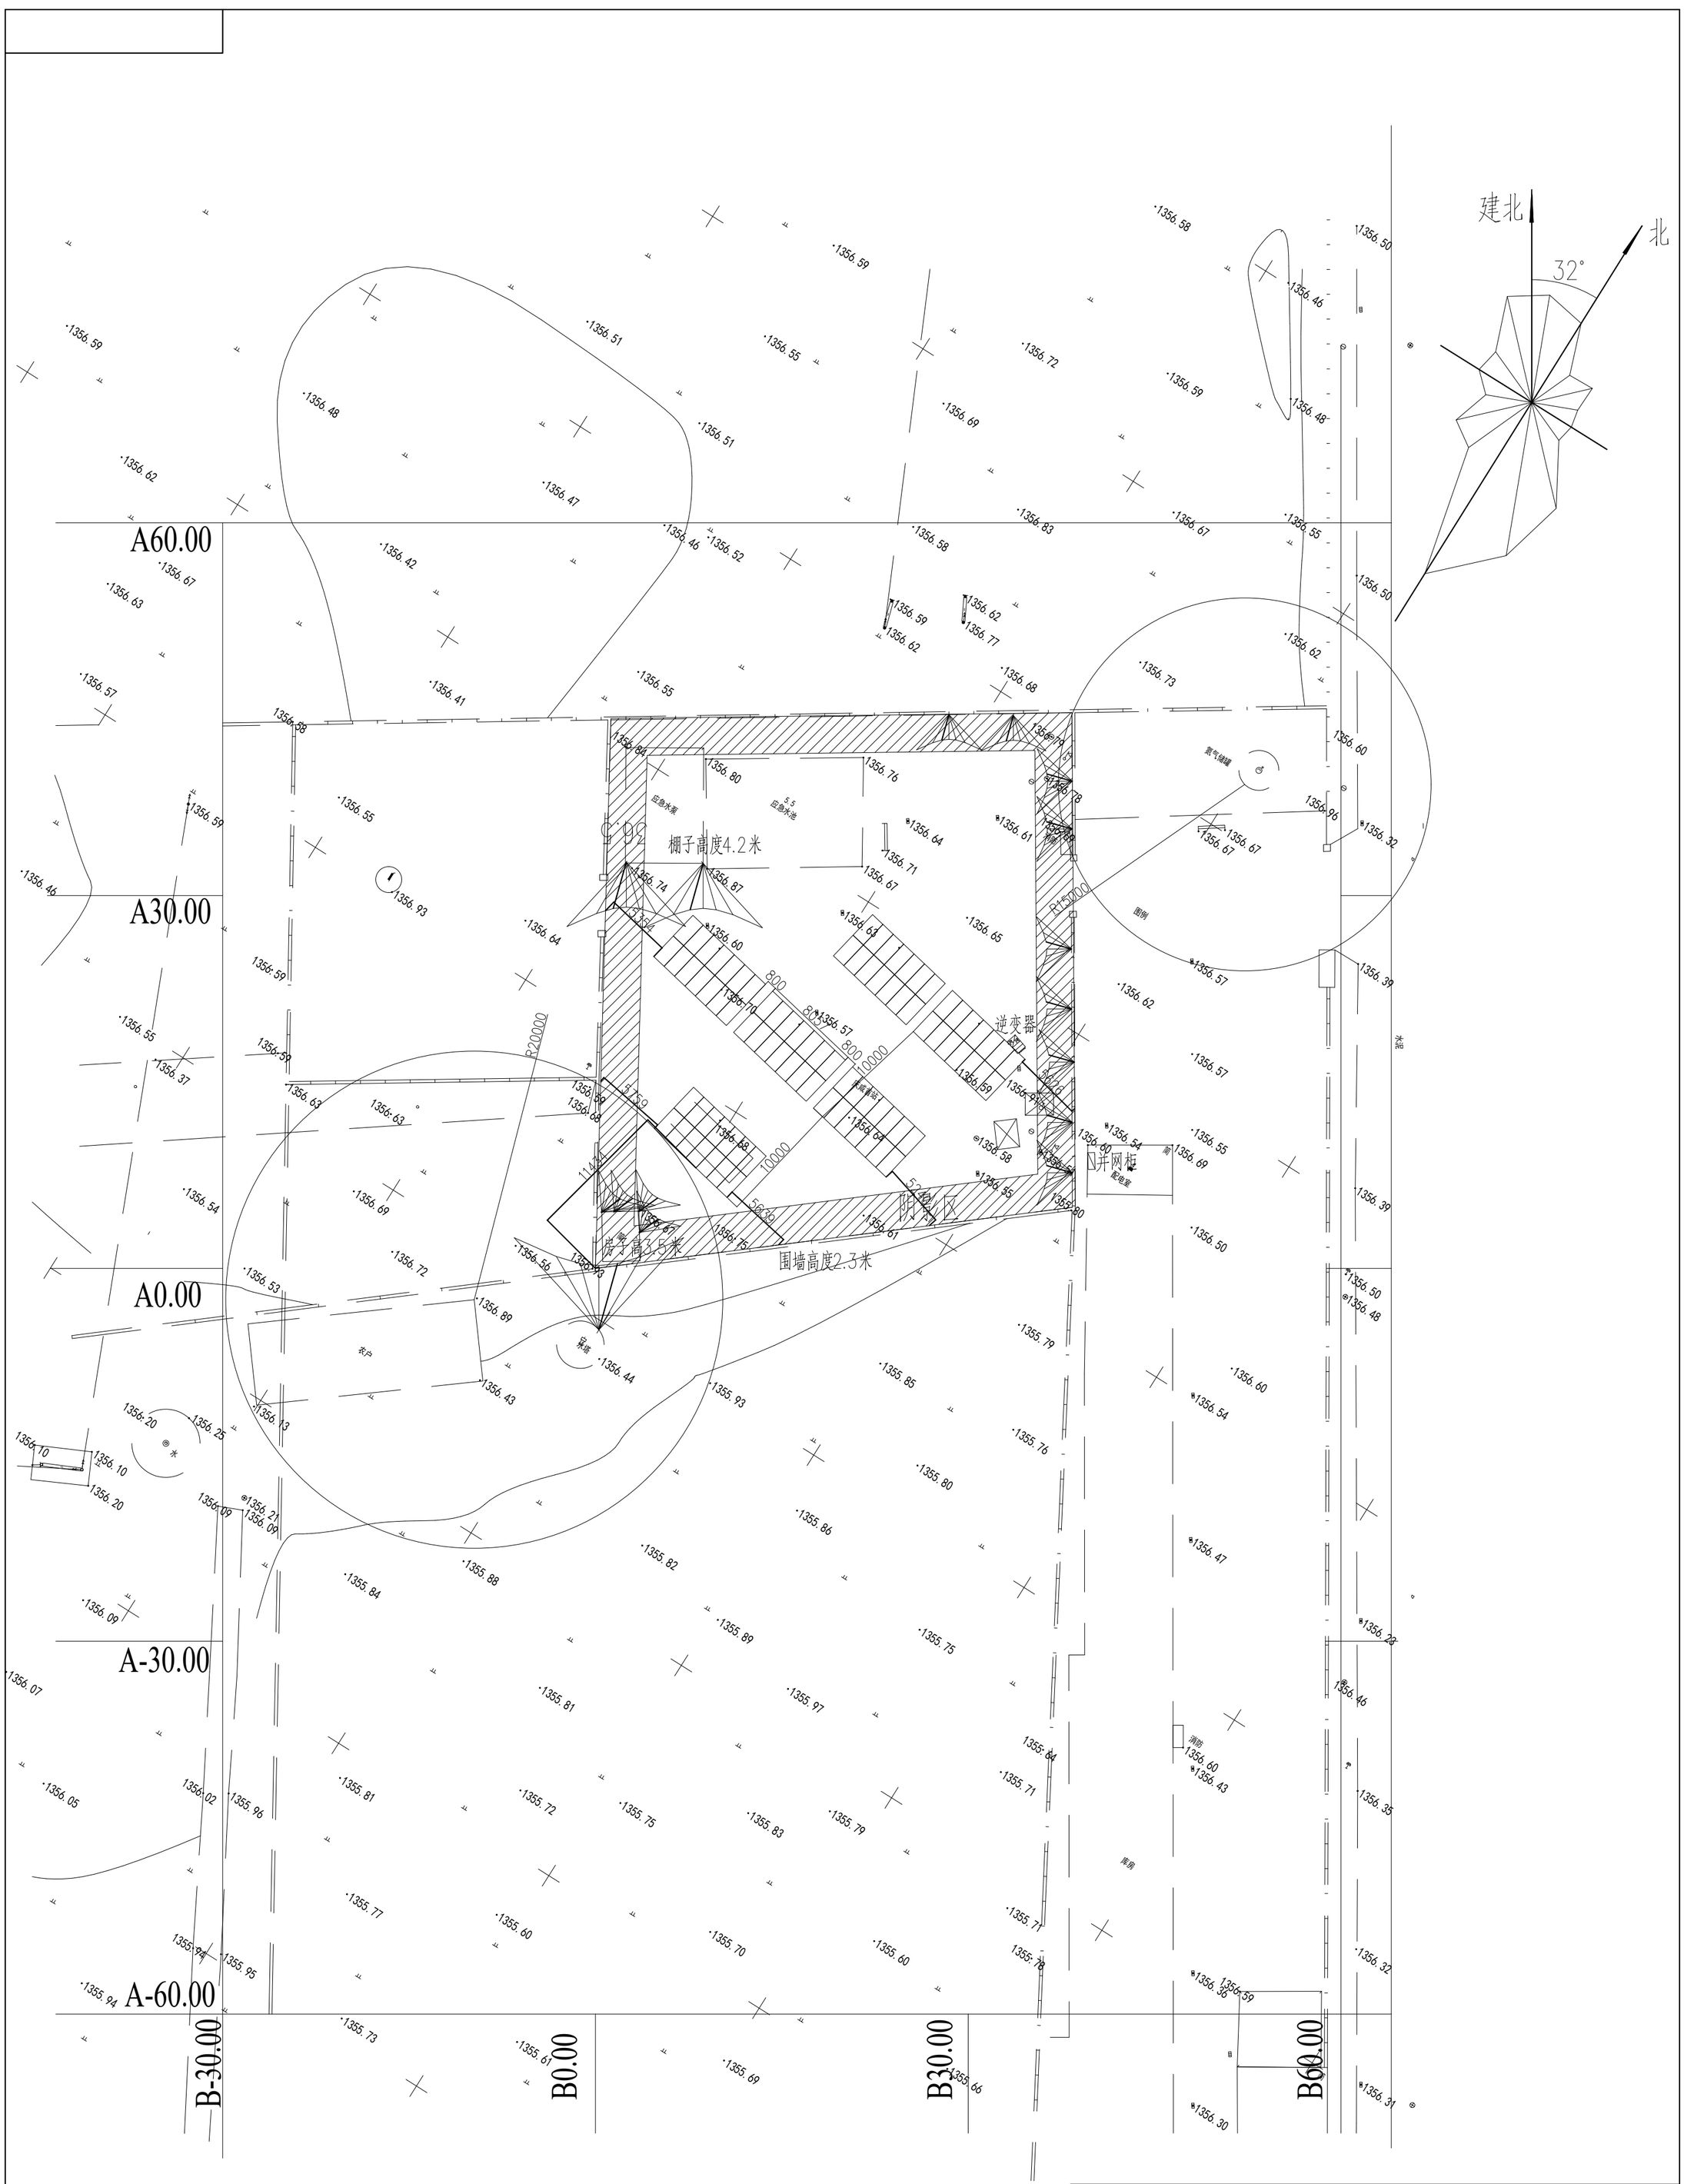


说明:

1.组件采用550Wp单晶硅双面双玻光伏组件，规格为2278×1134×35mm。

2.图中尺寸以mm计.

3.地面光伏组件采用33°倾角布置。

名称	组件排布角度	组件标称功率	组件数量	安装总容量	逆变器	
庆咸首站	33°	550Wp	84块	46.2kWp	40kW	1台

光伏组件及逆变器统计表

中国石油管道局工程有限公司

CHINA PETROLEUM PIPELINE ENGINEERING CORPORATION

工程设计综合甲级证书编号A113000069　工程勘察综合类甲级证书编号B113000069

制　图		长庆油田分公司第二输油处
设　计		
校　对		第二输油处2026年2座低效站点改造项目 庆咸首站
审　核		
		组件平面布置图
		阶 段 初设　文件号
		比 例 ~　项目号
		日 期 2026.1.29　版　次